


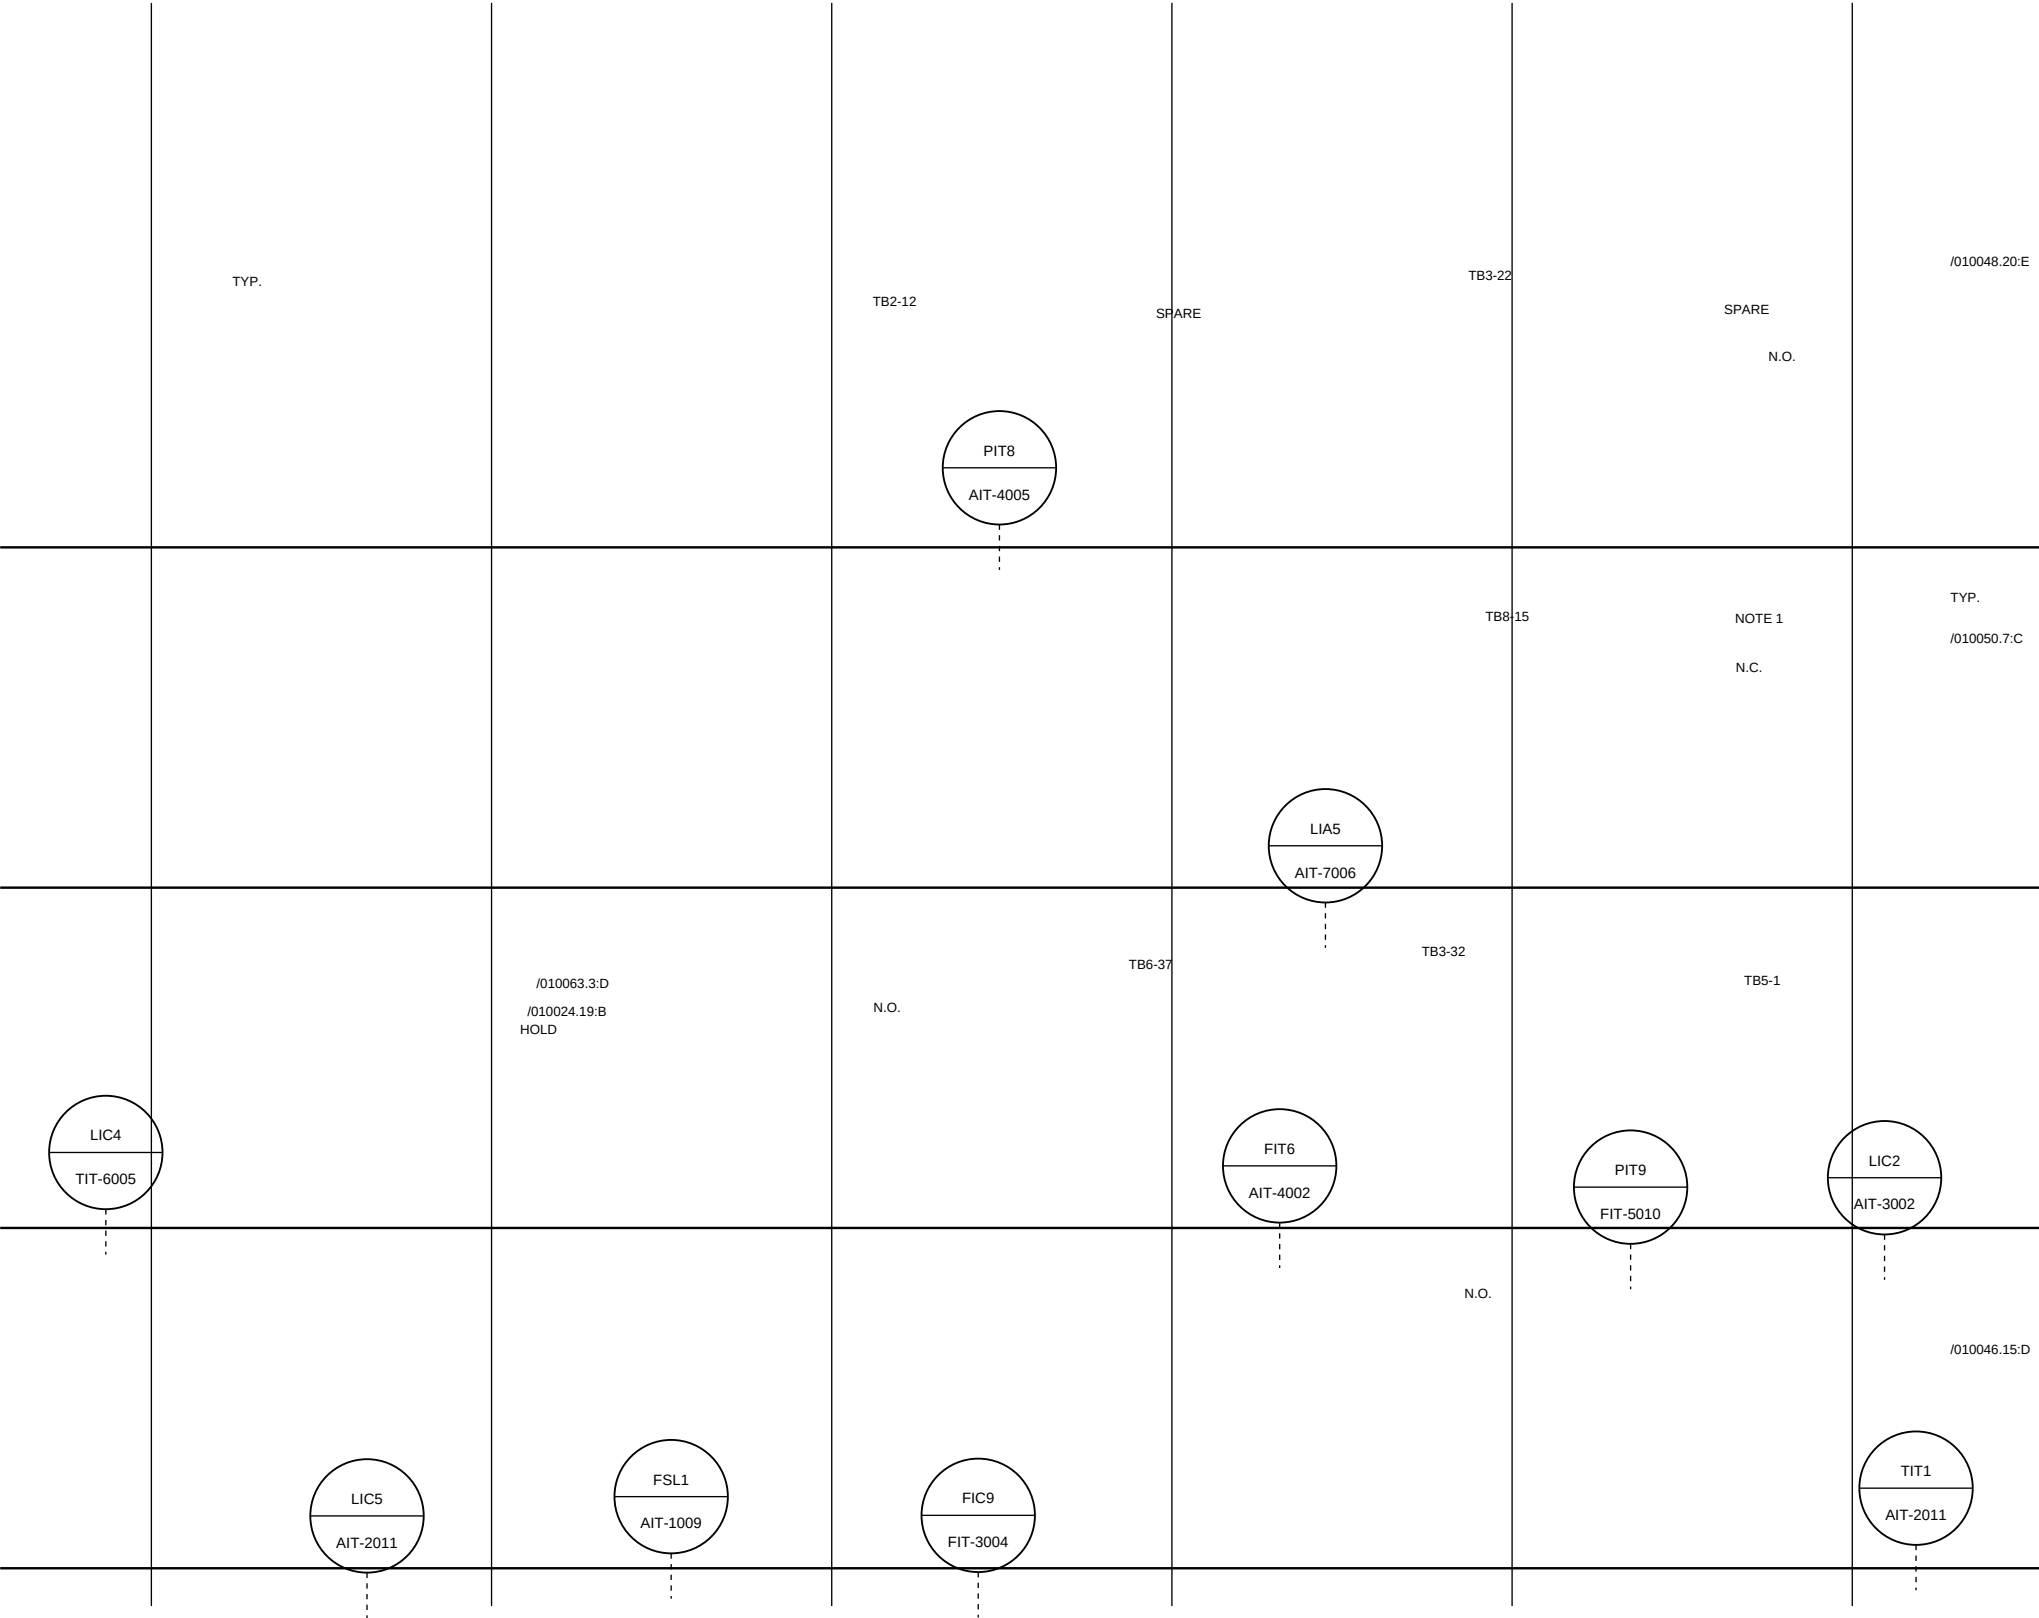


REV	DESCRIPTION	DATE	APP'D
A	ISSUED FOR REVIEW	26-03-11	DEM
B	ISSUED FOR APPROVAL	26-05-20	DEM
DWG. TITLE DEMO UPW SYSTEM PIPING & INSTRUMENT DIAGRAM FOR PRETREATMENT			
PROJECT TITLE DEMO WATER PLANT Ph1			
PROJECT NO. 99001D			
MAKER DEMO ENGINEERING CO., LTD.			
SHEET NO. DM-PNT1C01-UW-A20-010001			
REV B			

CARTRIDGE FILTER

TRANSFER PUMP

FEED PUMP

ISSUE
FOR APPROVAL

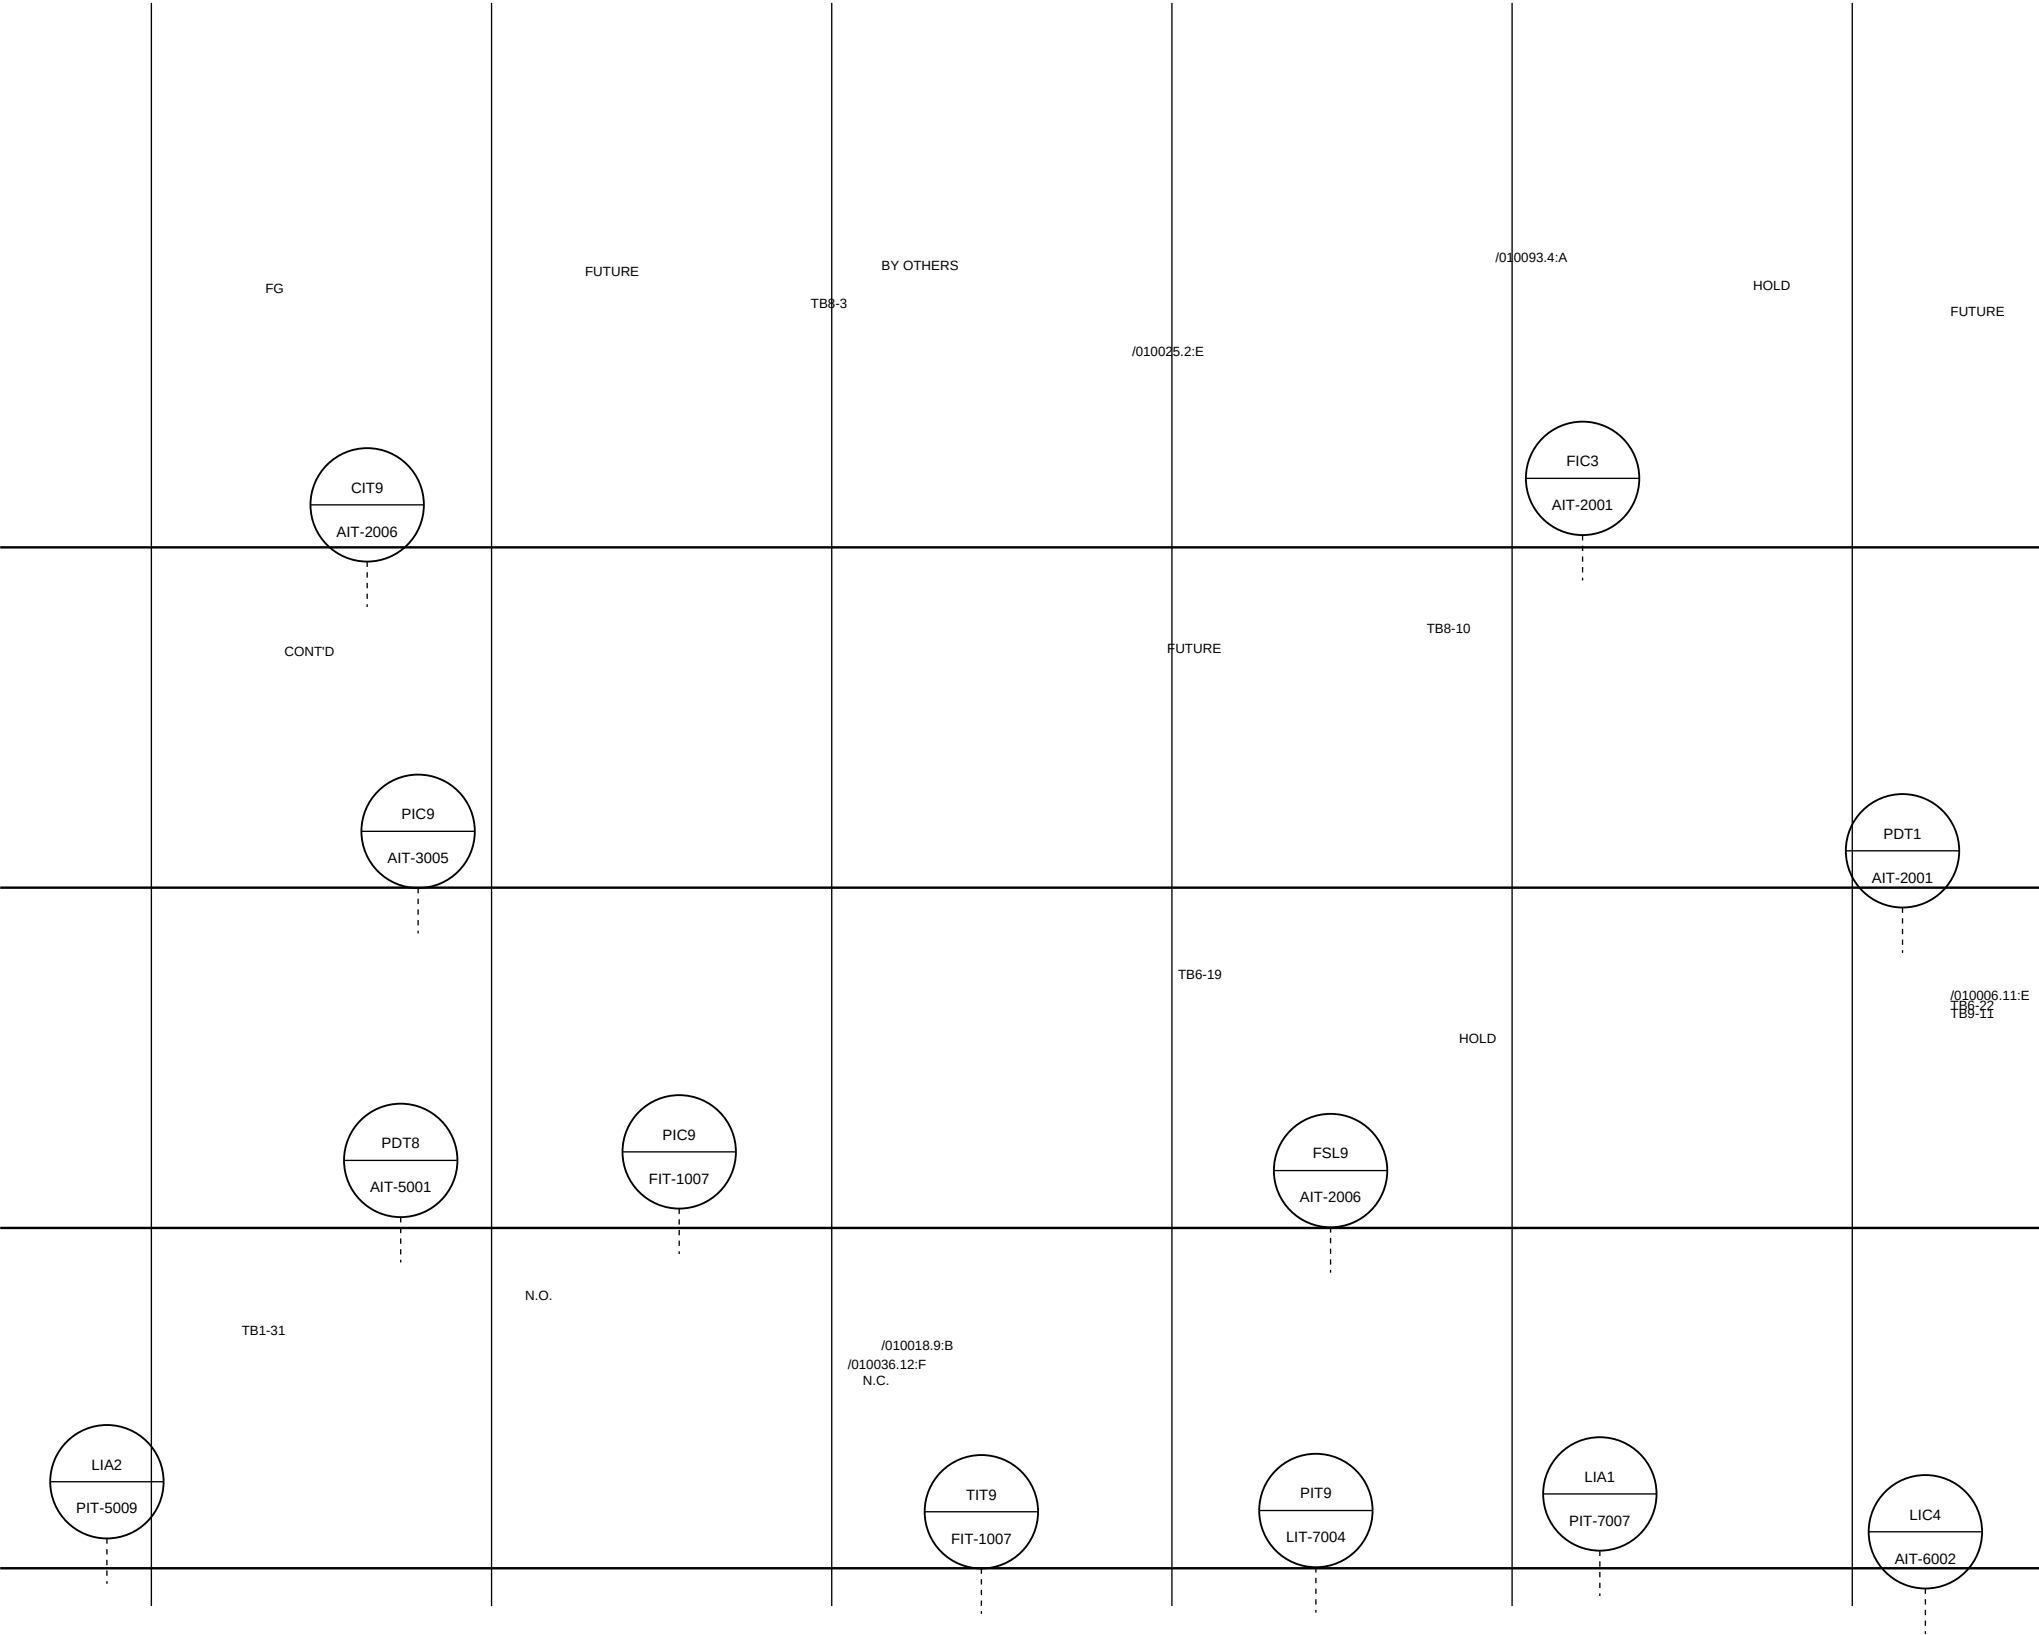


REV	DESCRIPTION	DATE	APP'D
A	ISSUED FOR REVIEW	26-03-11	DEM
B	ISSUED FOR APPROVAL	26-05-20	DEM
DWG. TITLE DEMO UPW SYSTEM PIPING & INSTRUMENT DIAGRAM FOR RO SYSTEM			
PROJECT TITLE DEMO WATER PLANT Ph1			
PROJECT NO. 99001D			
MAKER DEMO ENGINEERING CO., LTD.			
SHEET NO. DM-PNT1C01-UW-A20-010002			
REV			C

FEED PUMP

UF UNIT


RO SKID

ISSUE
FOR APPROVAL

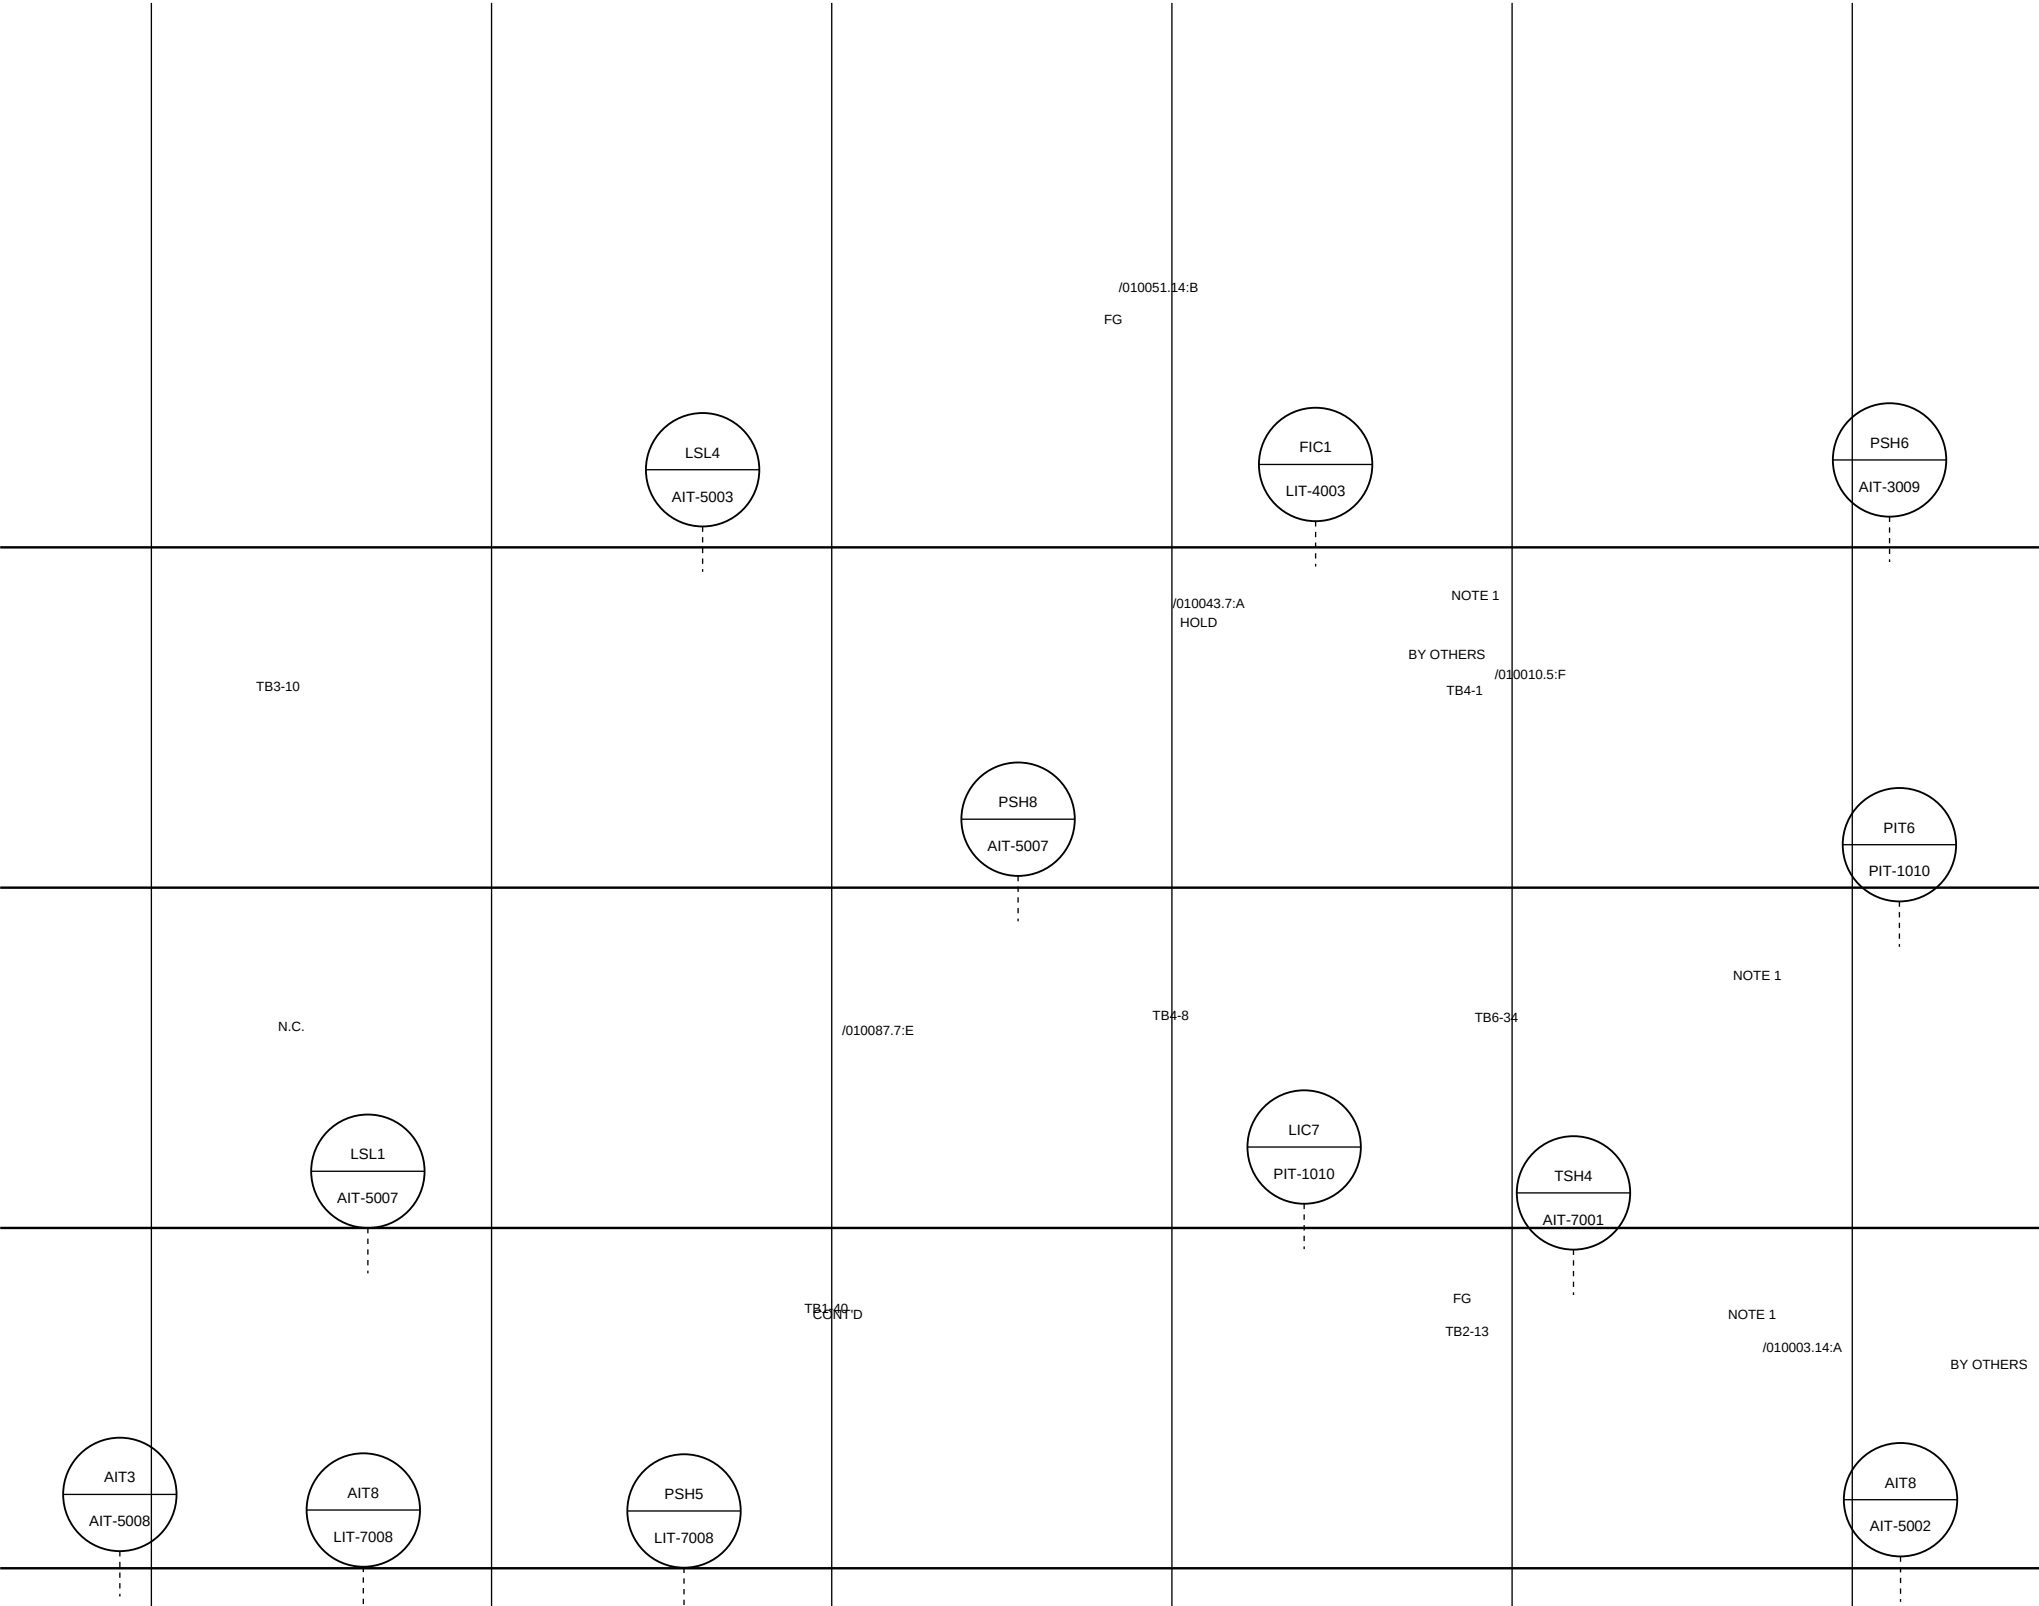


REV	DESCRIPTION	DATE	APP'D
A	ISSUED FOR REVIEW	26-03-11	DEM
B	ISSUED FOR APPROVAL	26-05-20	DEM
DWG. TITLE PROJECT TITLE PROJECT NO. MAKER SHEET NO. DEMO UPW SYSTEM PIPING & INSTRUMENT DIAGRAM FOR CEDI SYSTEM DEMO WATER PLANT Ph1 99001D DEMO ENGINEERING CO., LTD. DM-PNT1C01-UW-A20-010003			
REV			B

ISSUE
FOR APPROVAL

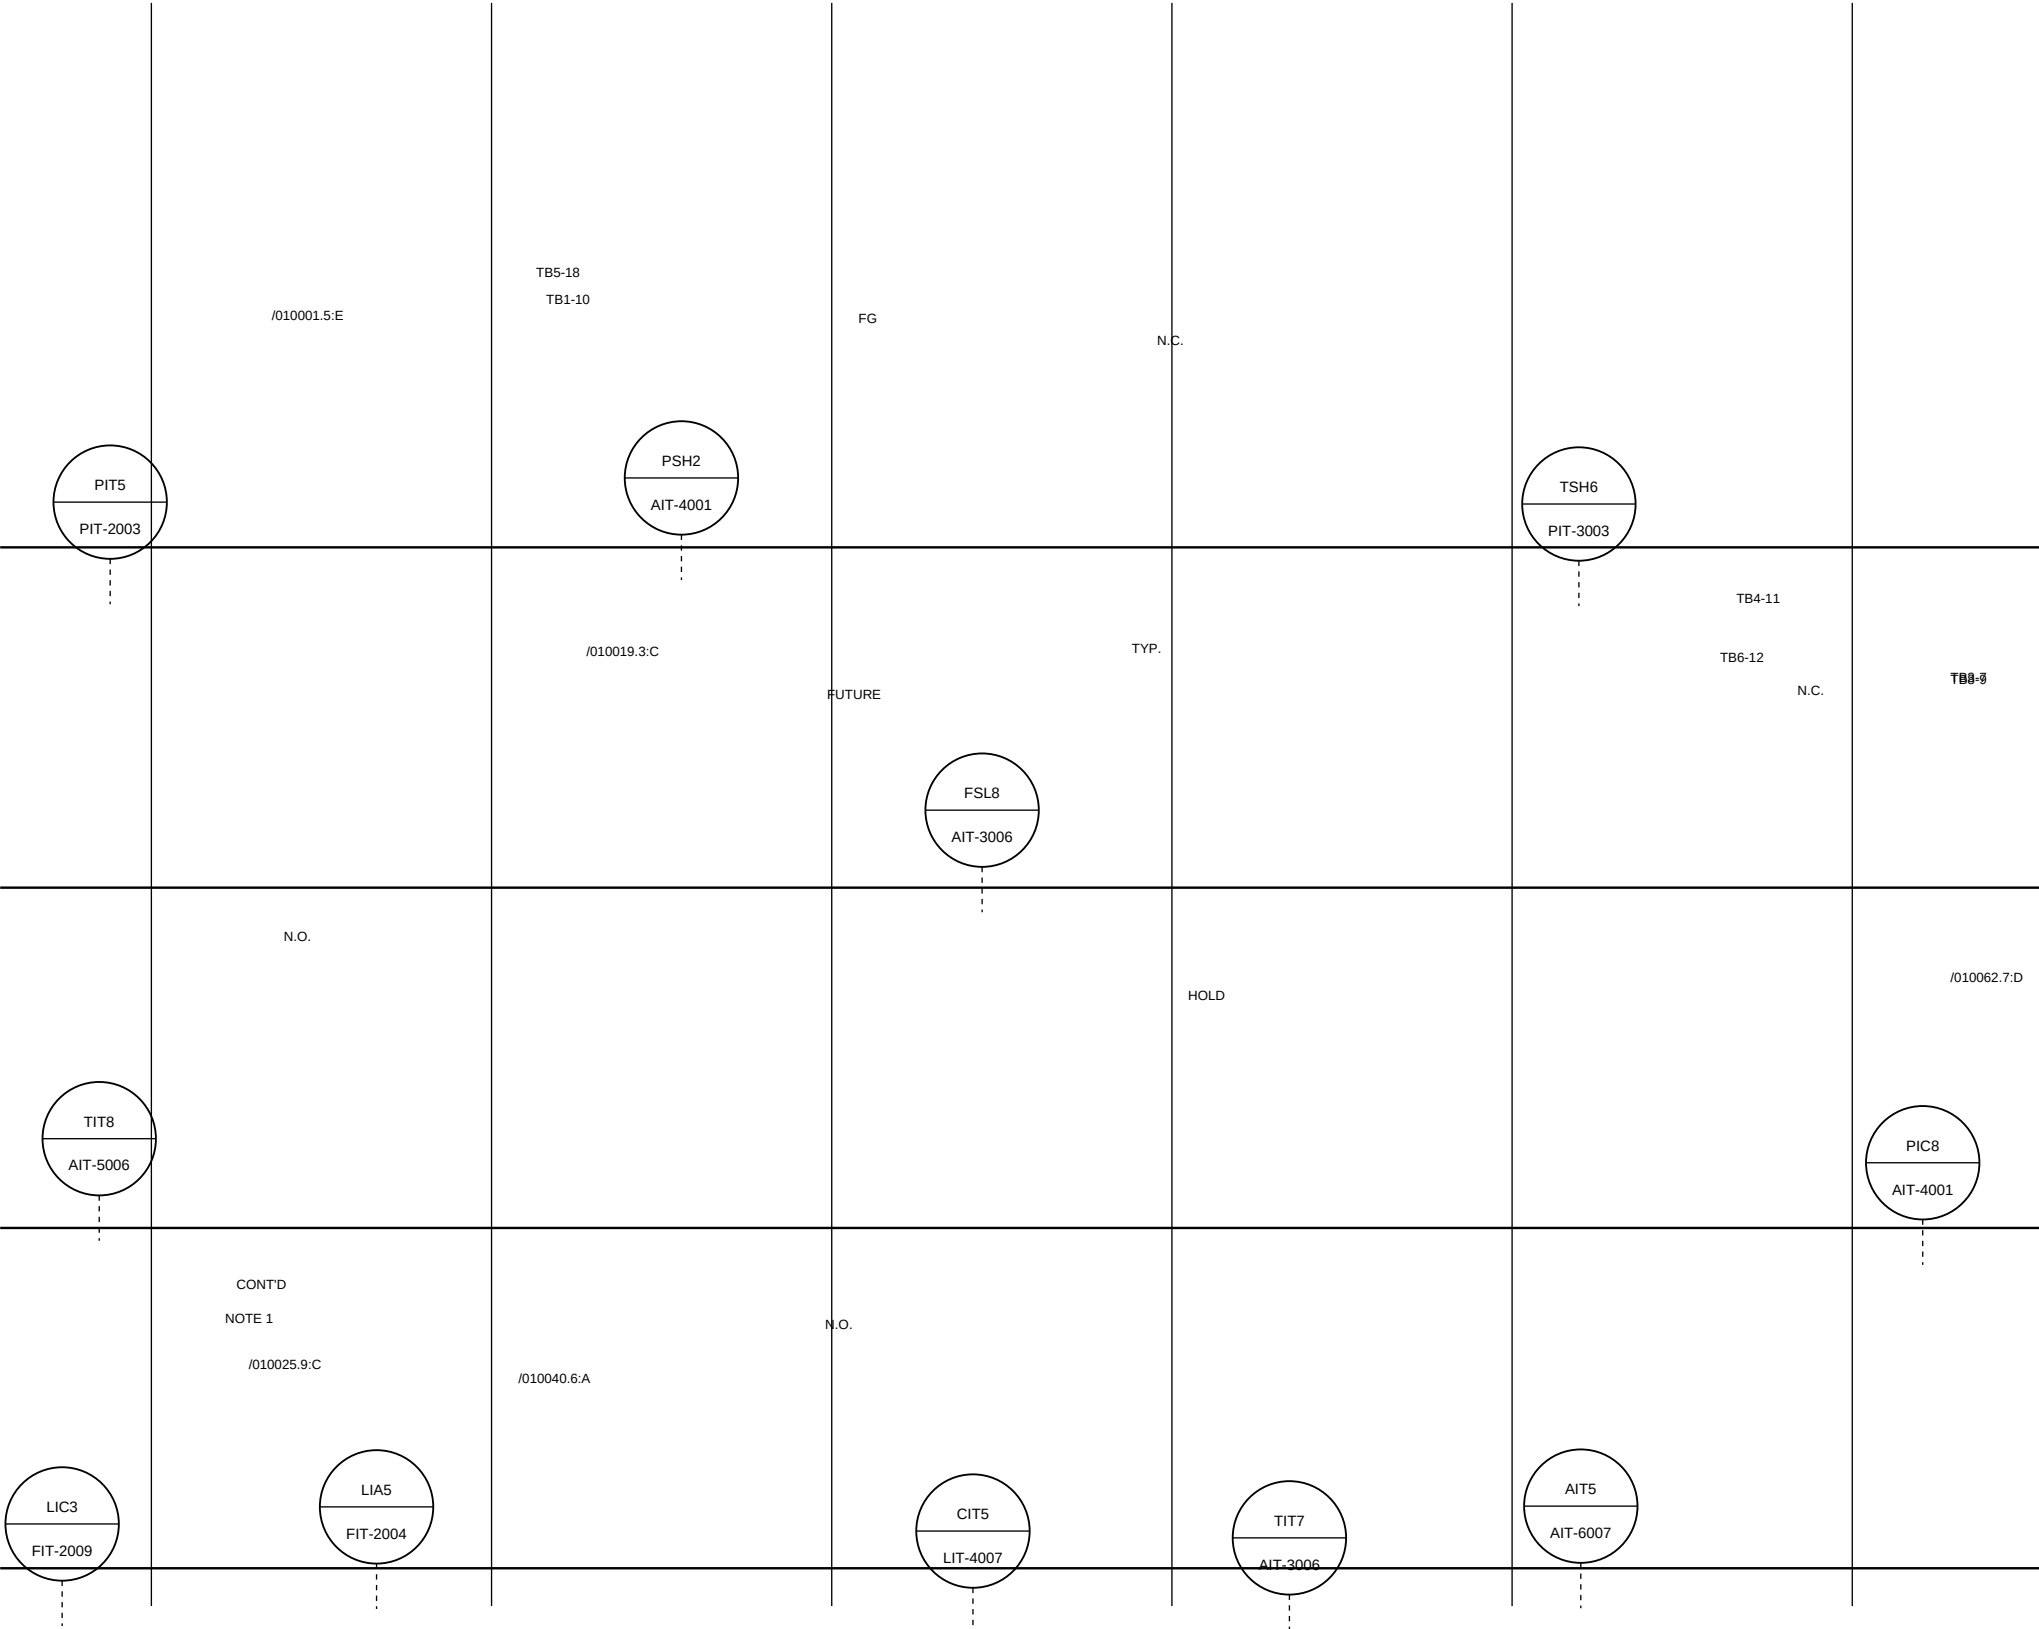


REV	DESCRIPTION	DATE	APP'D
A	ISSUED FOR REVIEW	26-03-11	DEM
B	ISSUED FOR APPROVAL	26-05-20	DEM
DWG. TITLE DEMO UPW SYSTEM PIPING & INSTRUMENT DIAGRAM FOR POLISHING LOOP			
PROJECT TITLE DEMO WATER PLANT Ph1			
PROJECT NO. 99001D			
MAKER DEMO ENGINEERING CO., LTD.			
SHEET NO. DM-PNT1C01-UW-A20-010004			
REV			C

ISSUE
FOR APPROVAL

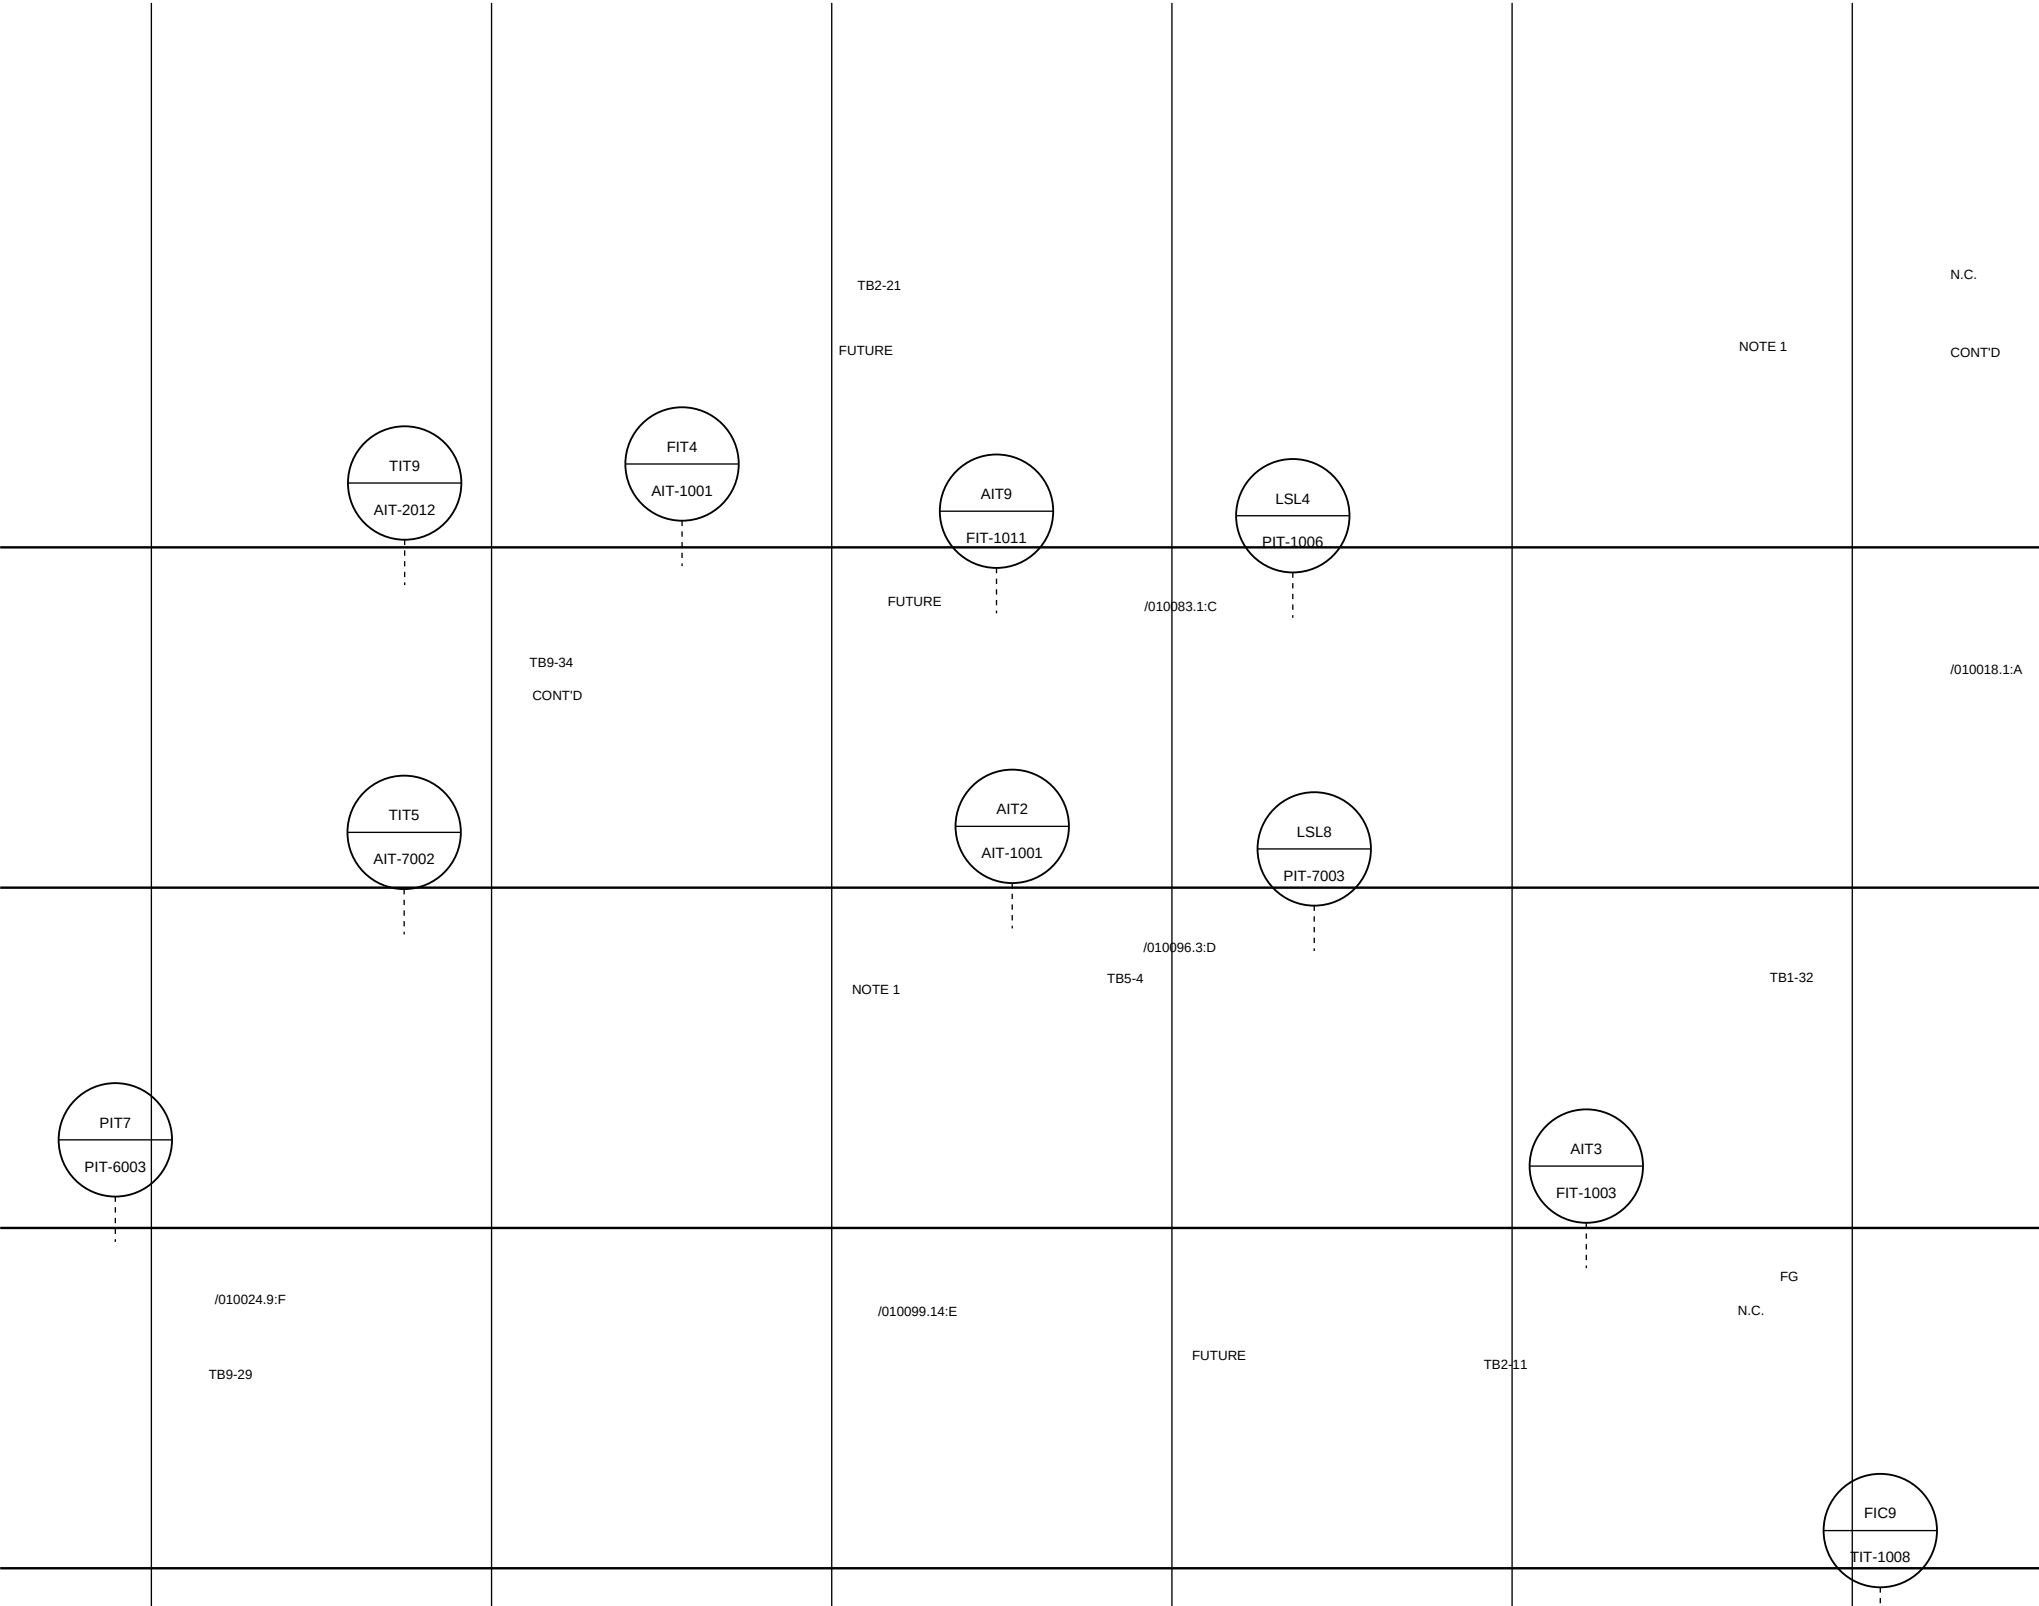


REV	DESCRIPTION	DATE	APP'D
A	ISSUED FOR REVIEW	26-03-11	DEM
B	ISSUED FOR APPROVAL	26-05-20	DEM
DWG. TITLE DEMO UPW SYSTEM PIPING & INSTRUMENT DIAGRAM FOR UPW TANK AREA			
PROJECT TITLE		DEMO WATER PLANT Ph1	
PROJECT NO.		99001D	
MAKER		DEMO ENGINEERING CO., LTD.	
SHEET NO.		DM-PNT1C01-UW-A20-010005	
REV A			

ISSUE
FOR APPROVAL

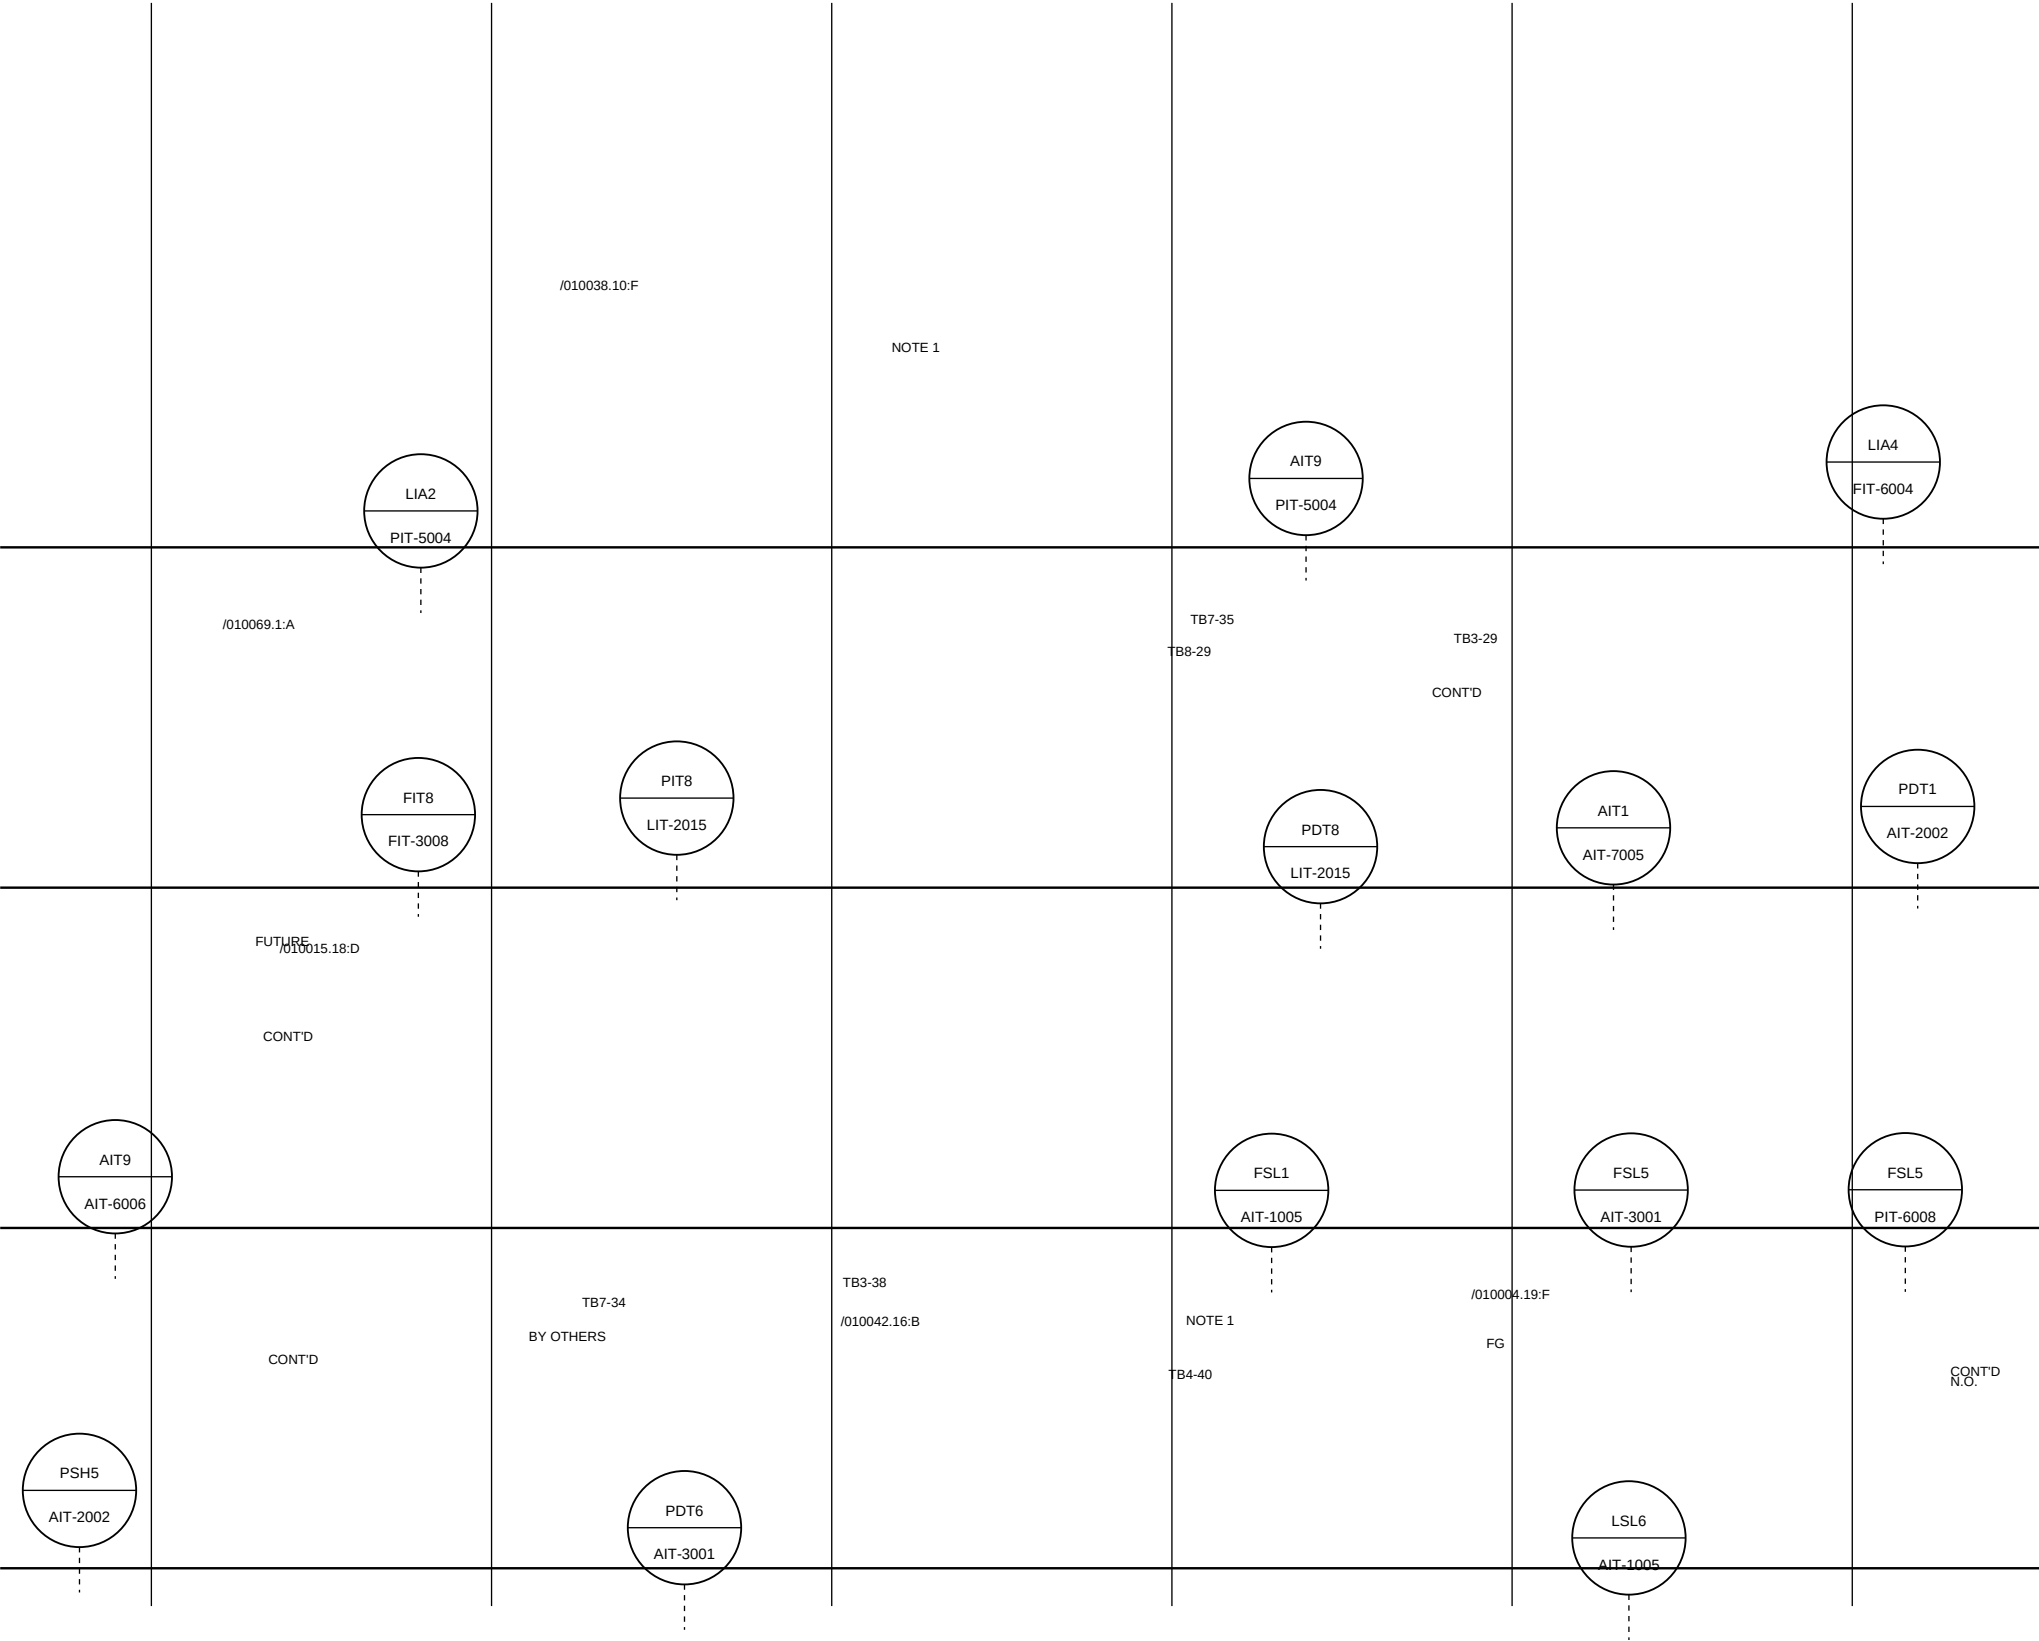


REV	DESCRIPTION	DATE	APP'D
A	ISSUED FOR REVIEW	26-03-11	DEM
B	ISSUED FOR APPROVAL	26-05-20	DEM
DWG. TITLE DEMO UPW SYSTEM PIPING & INSTRUMENT DIAGRAM FOR DISTRIBUTION LOOP			
PROJECT TITLE DEMO WATER PLANT Ph1			
PROJECT NO. 99001D			
MAKER DEMO ENGINEERING CO., LTD.			
SHEET NO. DM-PNT1C01-UW-A20-010006			
REV			A

ISSUE
FOR APPROVAL

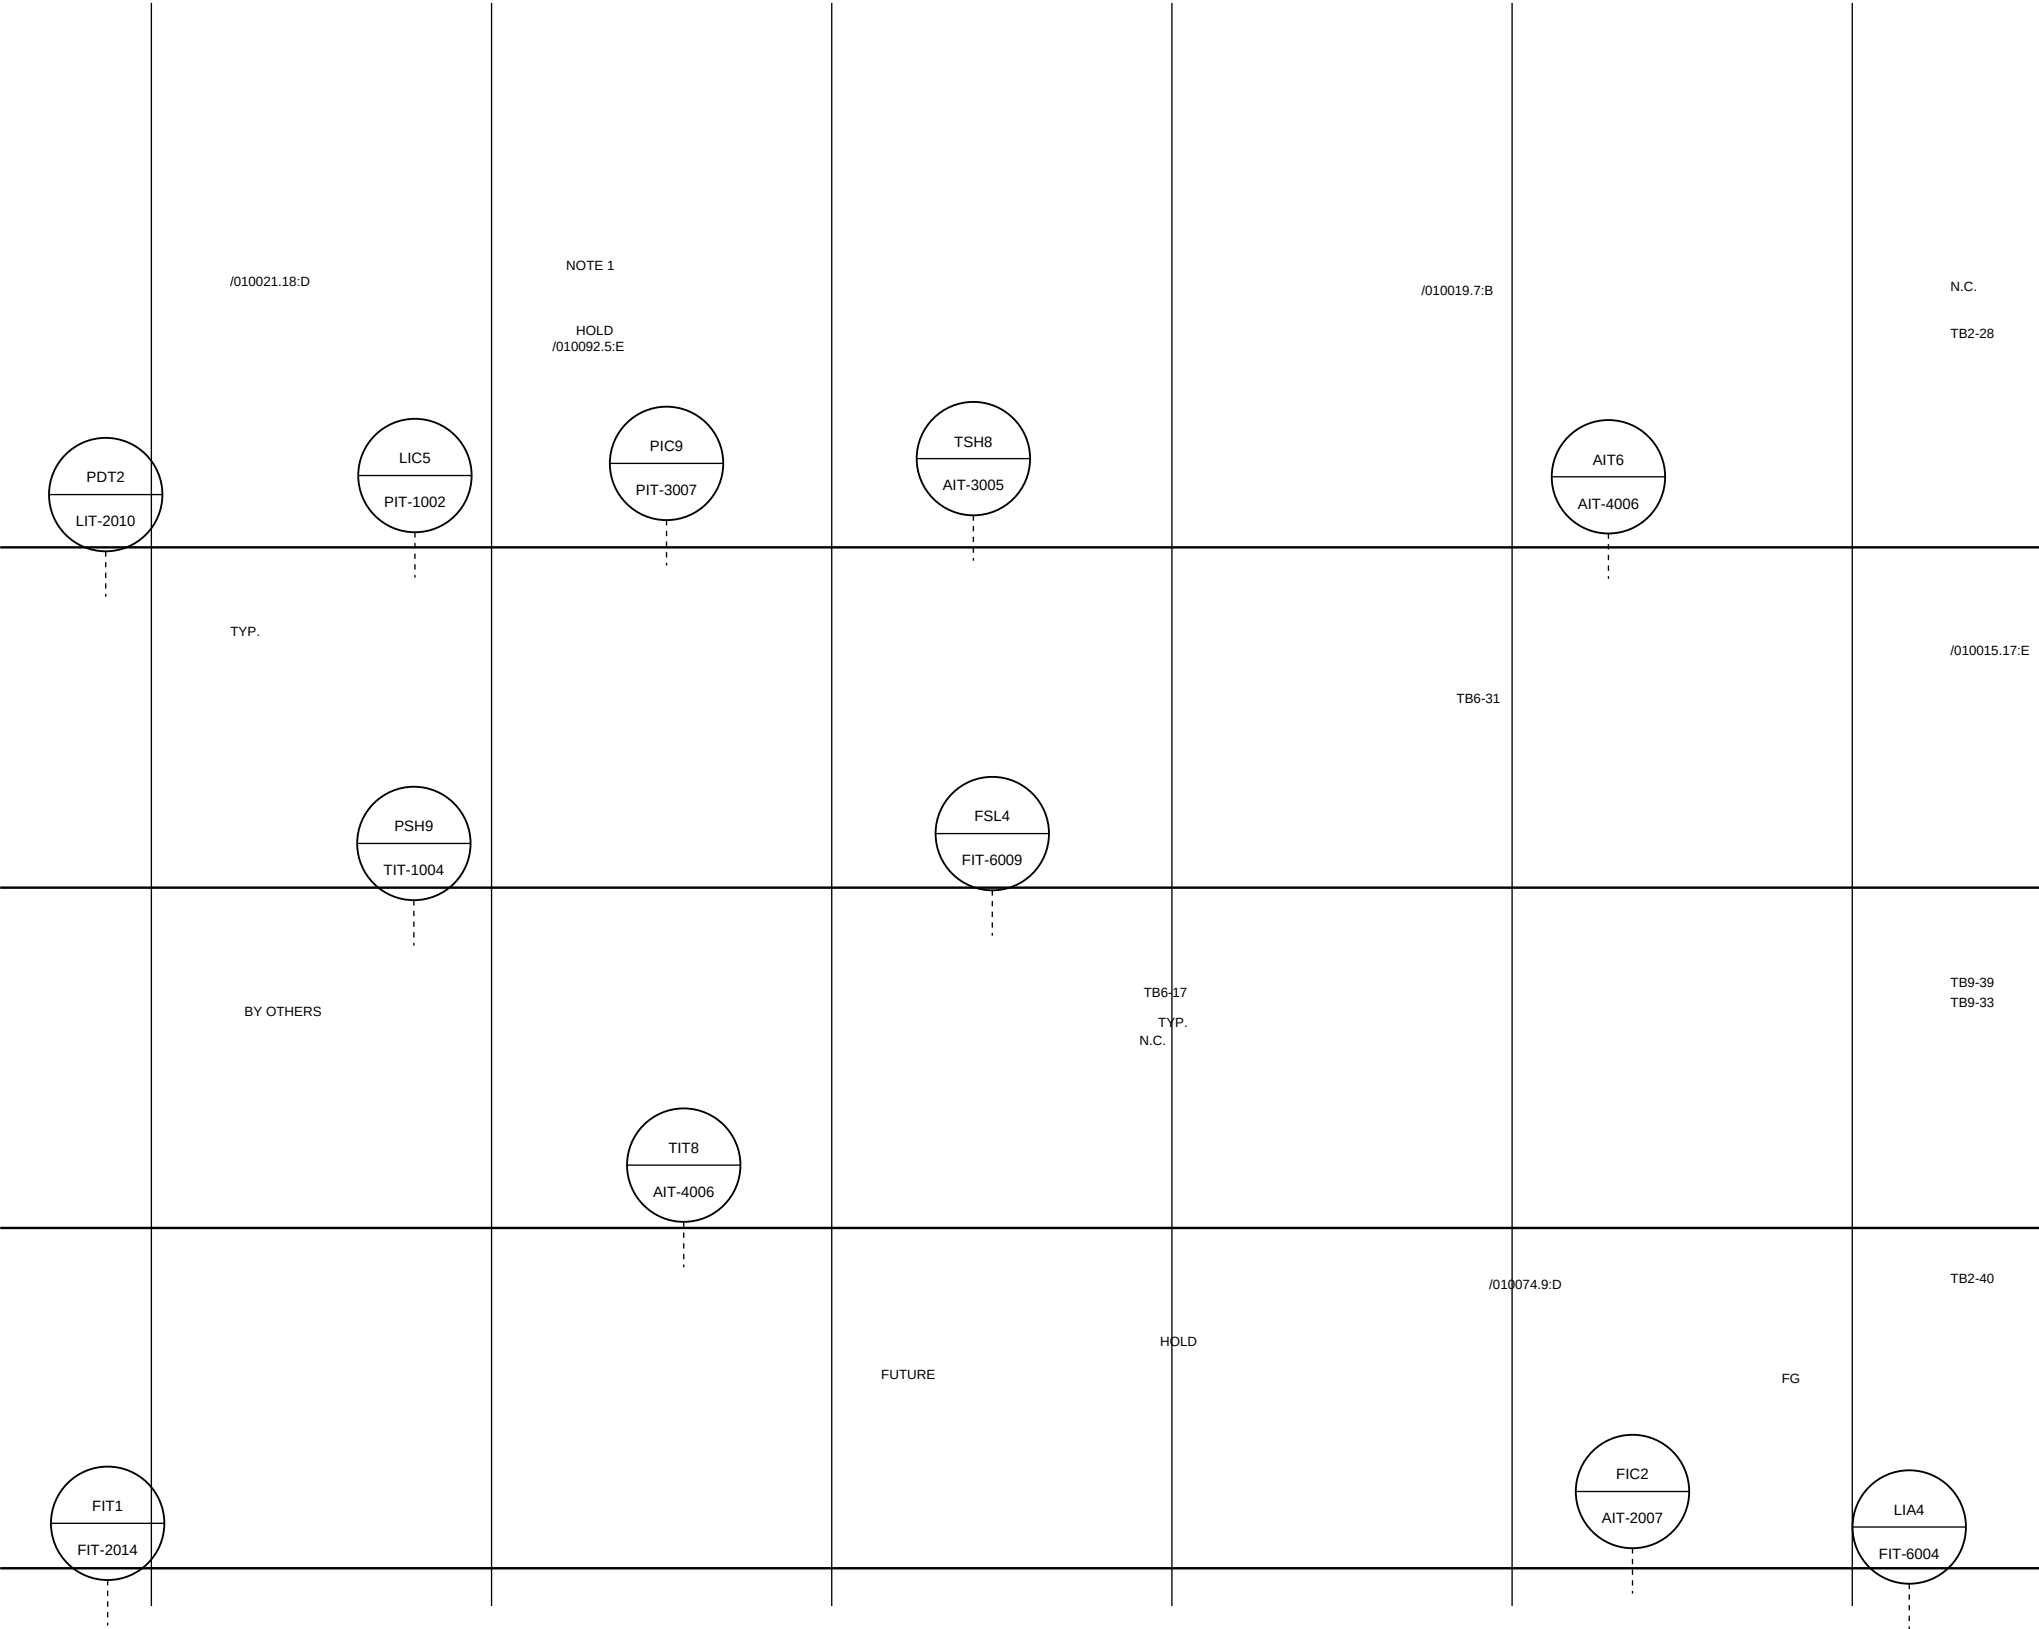

REV	DESCRIPTION	DATE	APP'D
A	ISSUED FOR REVIEW	26-03-11	DEM
B	ISSUED FOR APPROVAL	26-05-20	DEM
DWG. TITLE DEMO UPW SYSTEM PIPING & INSTRUMENT DIAGRAM FOR WASTE COLLECTION			
PROJECT TITLE DEMO WATER PLANT Ph1			
PROJECT NO. 99001D			
MAKER DEMO ENGINEERING CO., LTD.			
SHEET NO. DM-PNT1C01-UW-A20-010007			
REV			A

ISSUE
FOR APPROVAL

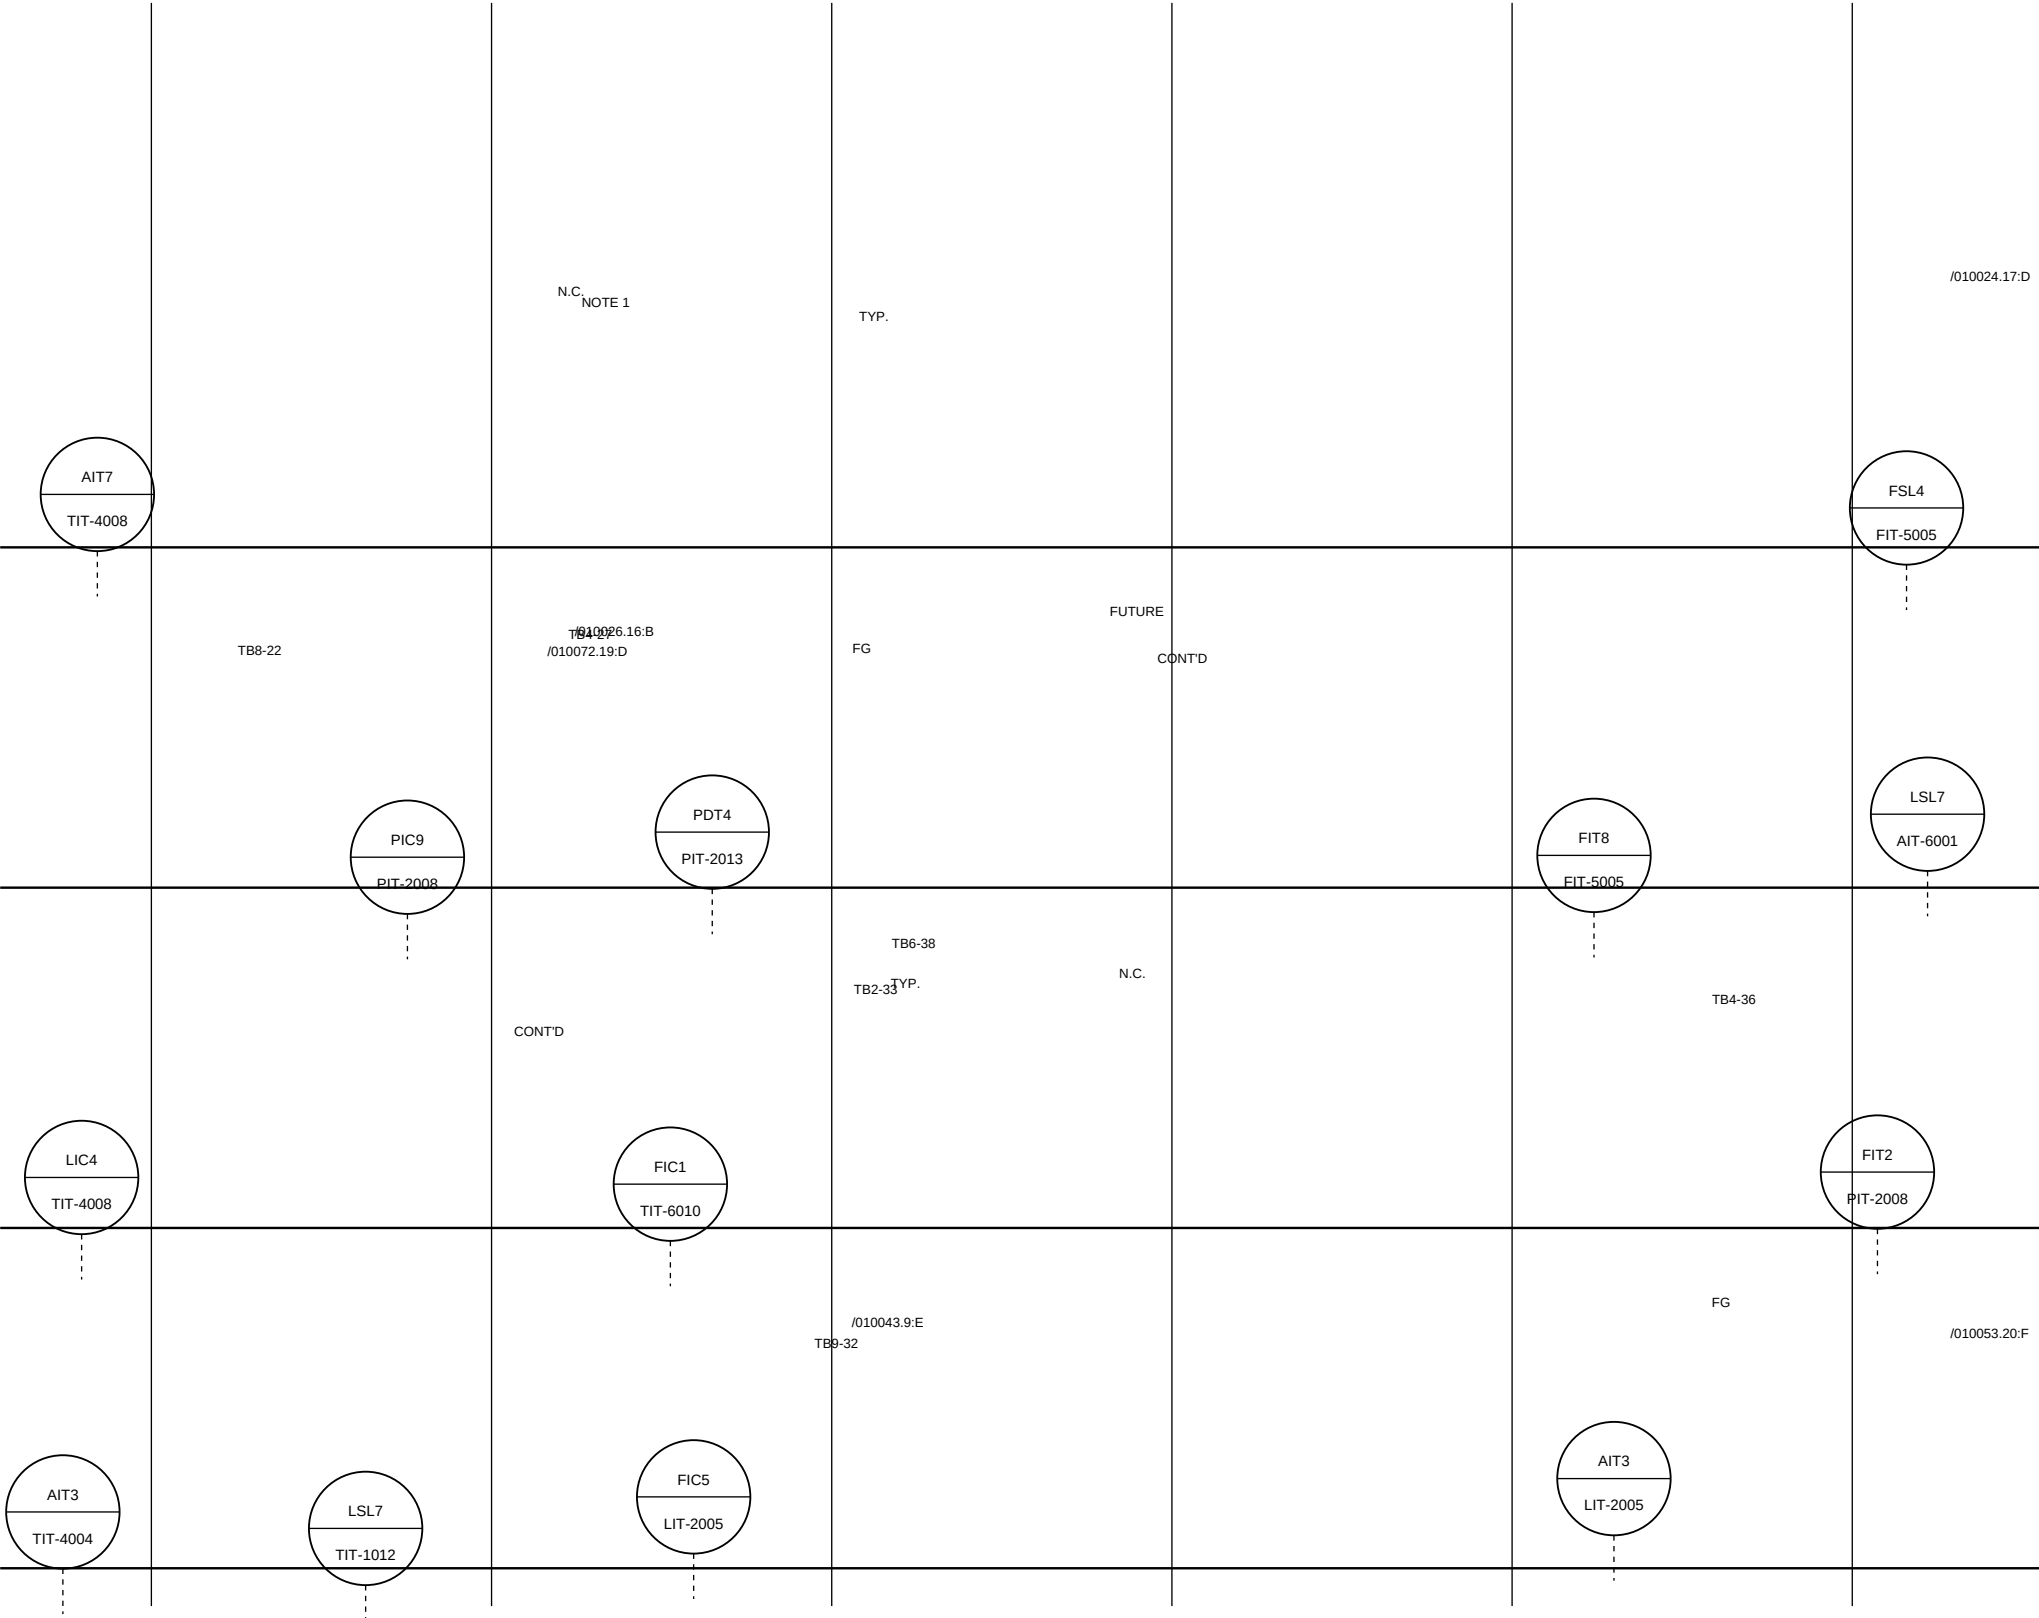

REV	DESCRIPTION	DATE	APP'D
A	ISSUED FOR REVIEW	26-03-11	DEM
B	ISSUED FOR APPROVAL	26-05-20	DEM
DWG. TITLE PROJECT TITLE PROJECT NO. MAKER SHEET NO. DEMO UPW SYSTEM PIPING & INSTRUMENT DIAGRAM FOR CHEMICAL DOSING DEMO WATER PLANT Ph1 99001D DEMO ENGINEERING CO., LTD. DM-PNT1C01-UW-A20-010008 REV B			

ISSUE

FOR APPROVAL