
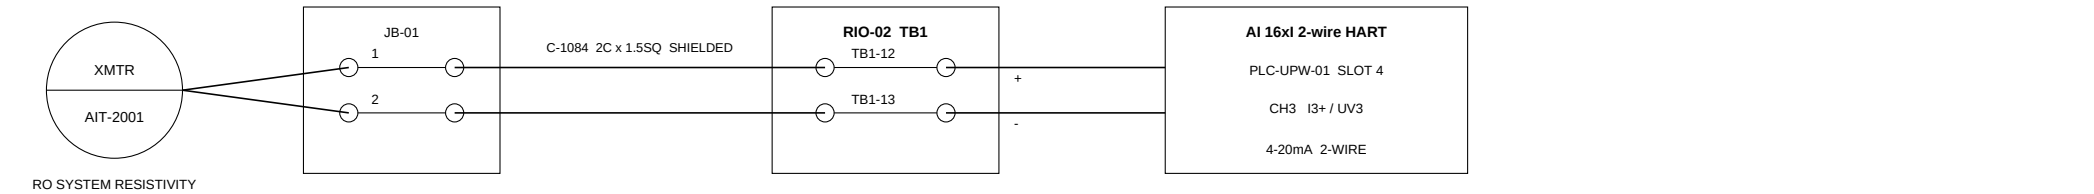
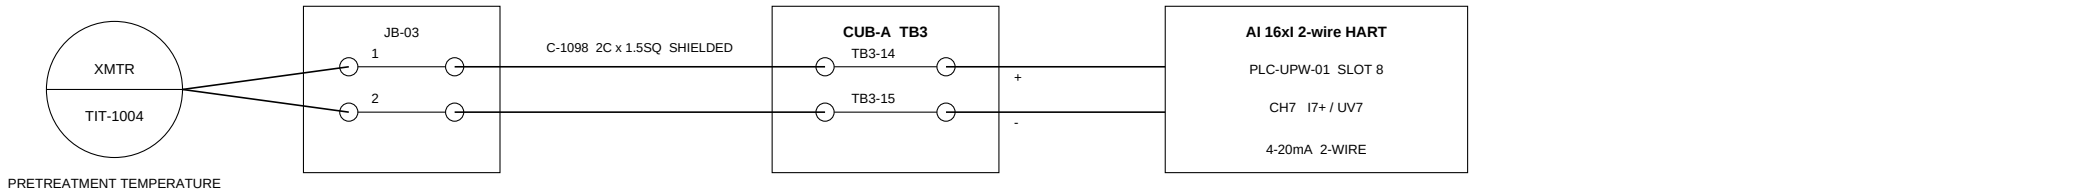
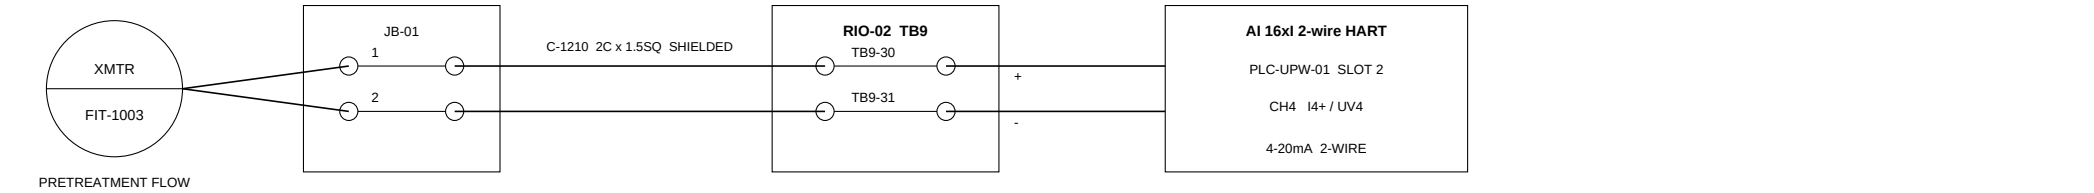
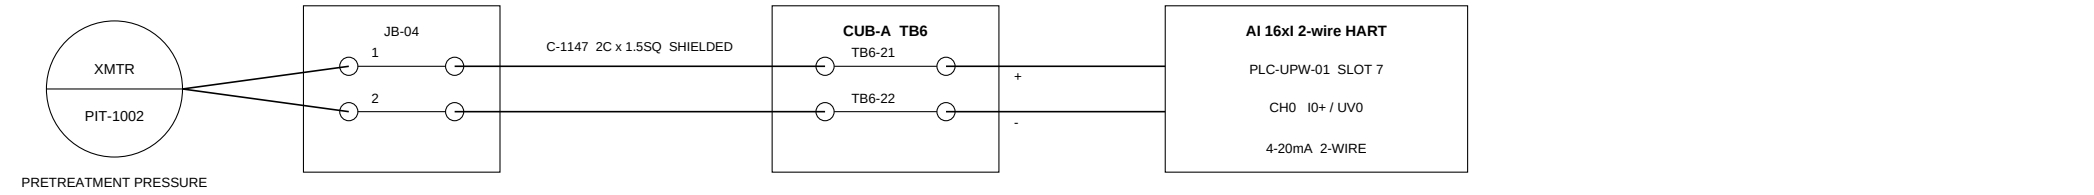


LOOP WIRING DIAGRAM / PRETREATMENT






FIELD INSTRUMENT JUNCTION BOX PANEL TERMINAL BLOCK I/O MODULE

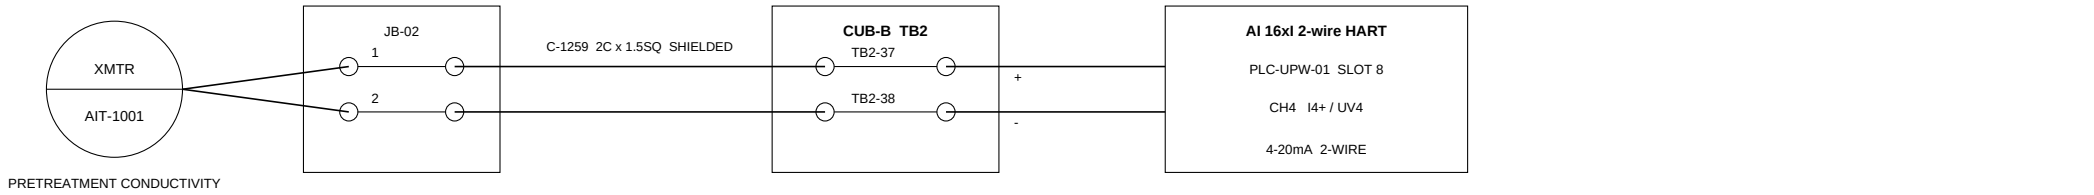

REV B ISSUED FOR APPROVAL 26-05-20 DEM			
DWG. TITLE	DEMO UPW SYSTEM LOOP WIRING DIAGRAM FOR PRETREATMENT		
PROJECT TITLE	DEMO WATER PLANT Ph1		
PROJECT NO.	99001D		
MAKER	DEMO ENGINEERING CO., LTD.		
SHEET NO.	DM-PNT1C01-UW-E30-020001		REV B

LOOP WIRING DIAGRAM / RO SYSTEM

FIELD INSTRUMENT JUNCTION BOX PANEL TERMINAL BLOCK I/O MODULE

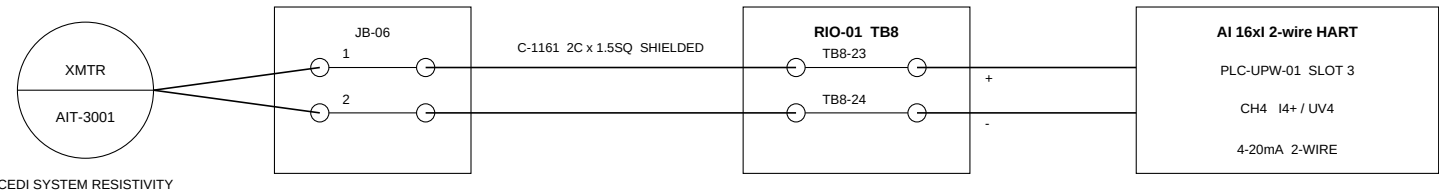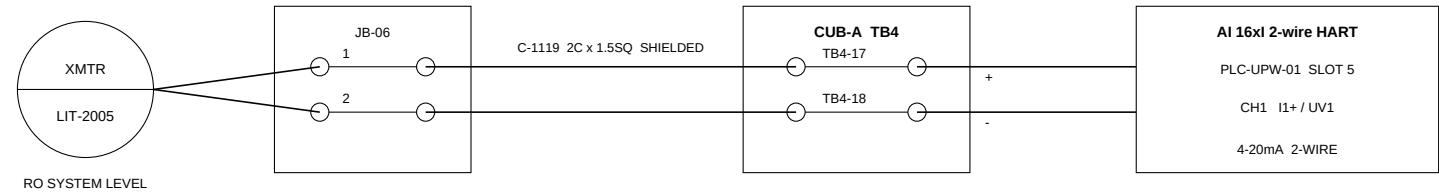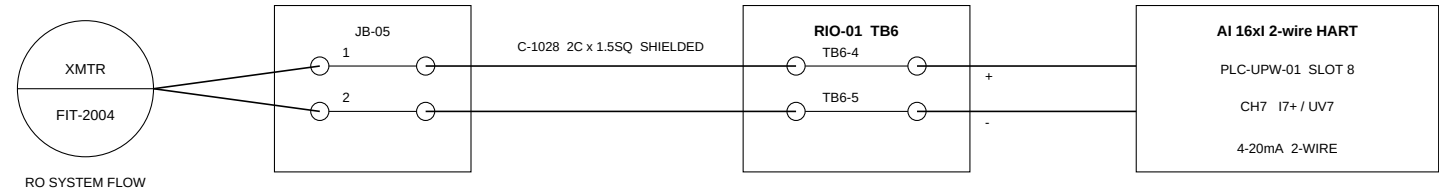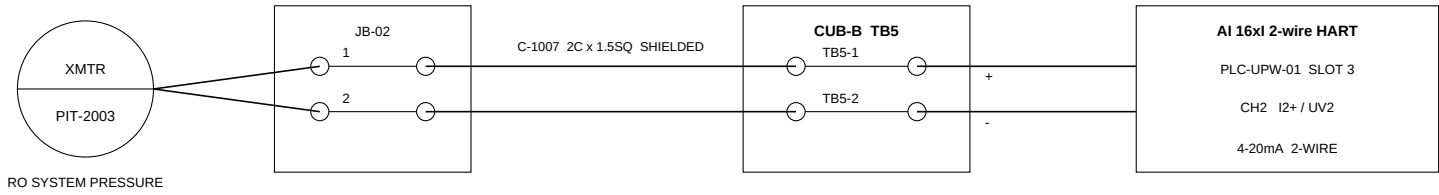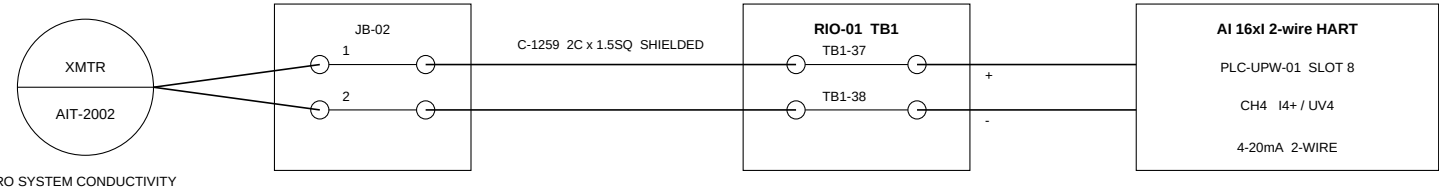

REV B ISSUED FOR APPROVAL 26-05-20 DEM

DWG. TITLE DEMO UPW SYSTEM
LOOP WIRING DIAGRAM FOR
RO SYSTEM

PROJECT TITLE DEMO WATER PLANT Ph1

PROJECT NO. 99001D


MAKER DEMO ENGINEERING CO., LTD.

SHEET NO. DM-PNT1C01-UW-E30-020002


REV B

LOOP WIRING DIAGRAM / CEDI SYSTEM


FIELD INSTRUMENT JUNCTION BOX PANEL TERMINAL BLOCK I/O MODULE

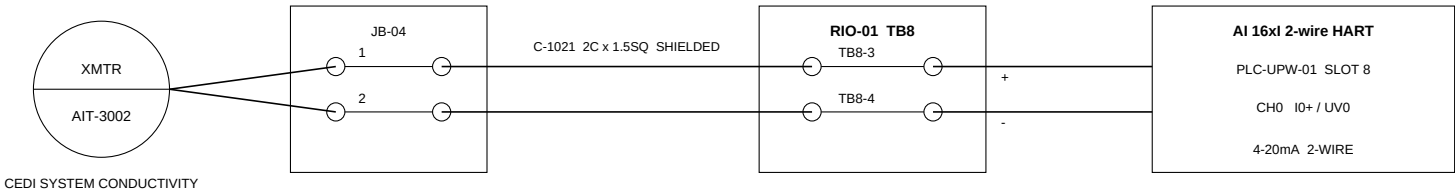


CEDI SYSTEM CONDUCTIVITY

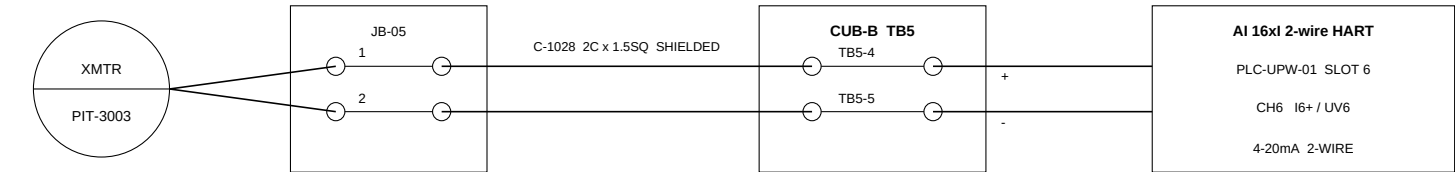


CEDI SYSTEM PRESSURE

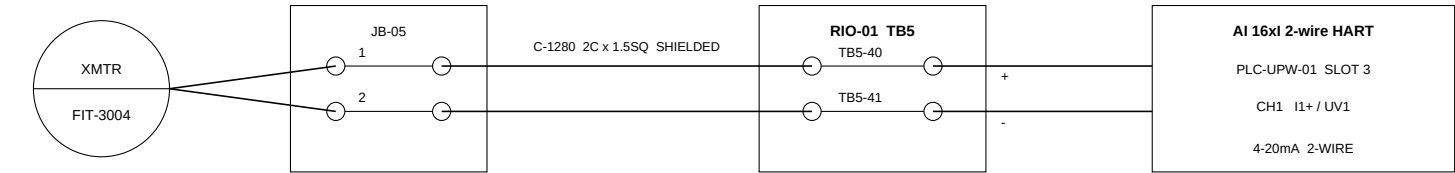

CEDI SYSTEM FLOW

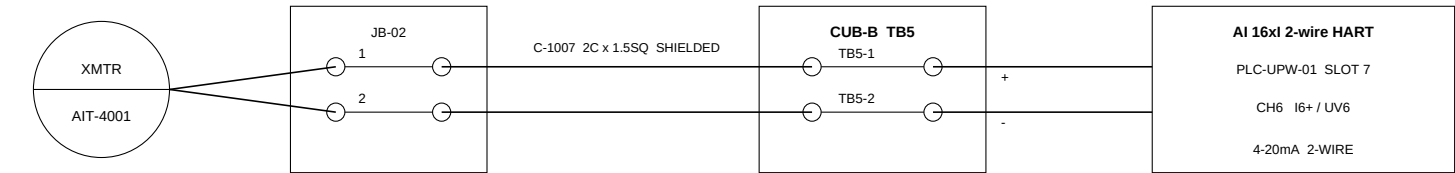

UPW TANK RESISTIVITY

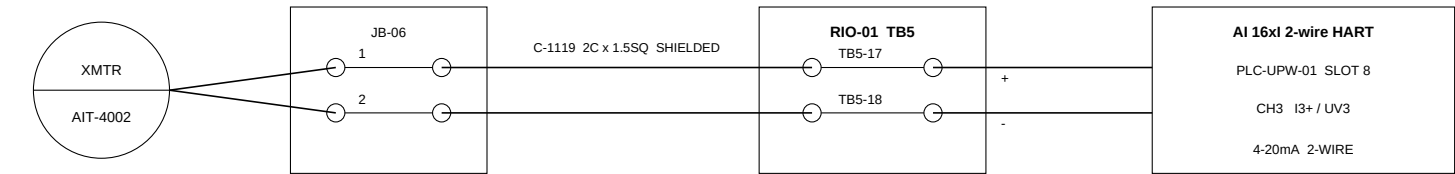

UPW TANK TOC

REV B ISSUED FOR APPROVAL 26-05-20 DEM

DWG. TITLE DEMO UPW SYSTEM
LOOP WIRING DIAGRAM FOR
CEDI SYSTEM






PROJECT TITLE DEMO WATER PLANT Ph1
PROJECT NO. 99001D
MAKER DEMO ENGINEERING CO., LTD.

SHEET NO. DM-PNT1C01-UW-E30-020003

REV B

LOOP WIRING DIAGRAM / UPW TANK






FIELD INSTRUMENT JUNCTION BOX PANEL TERMINAL BLOCK I/O MODULE

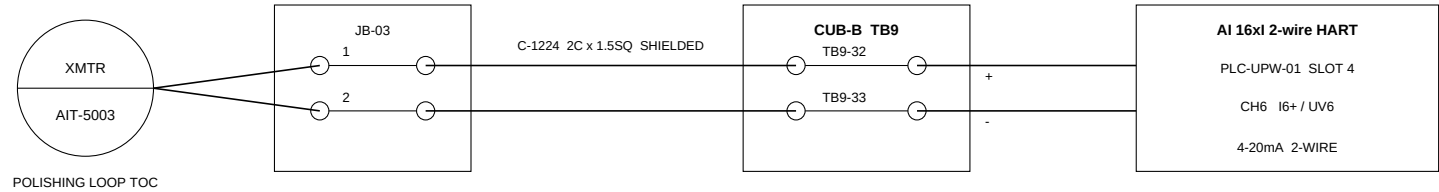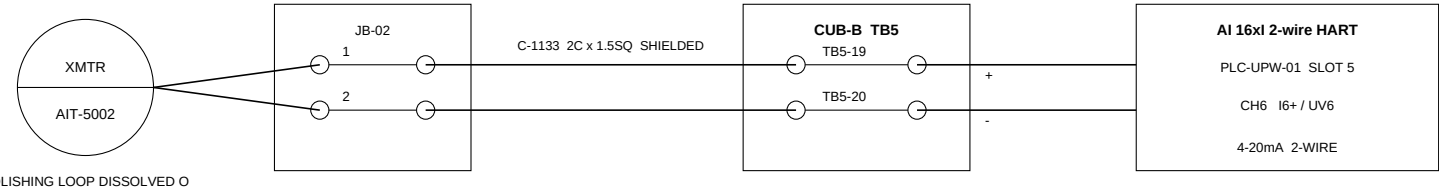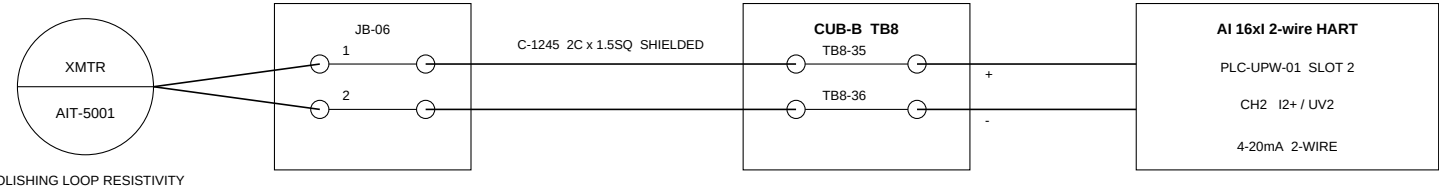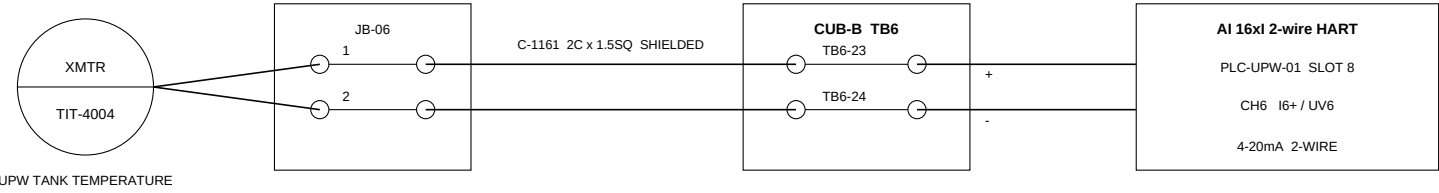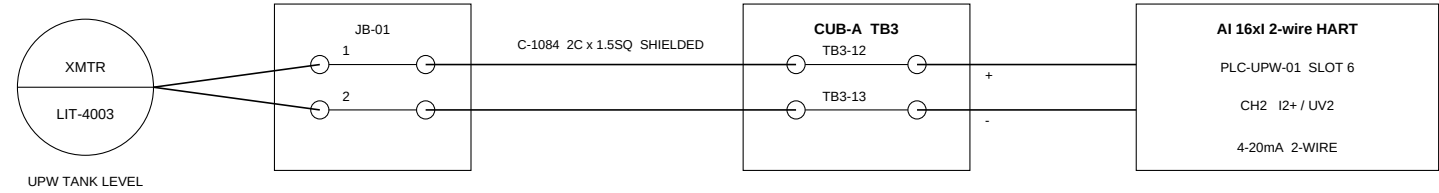

REV B ISSUED FOR APPROVAL 26-05-20 DEM			
DWG. TITLE	DEMO UPW SYSTEM LOOP WIRING DIAGRAM FOR UPW TANK		
PROJECT TITLE	DEMO WATER PLANT Ph1		
PROJECT NO.	99001D		
MAKER	DEMO ENGINEERING CO., LTD.		
SHEET NO.	DM-PNT1C01-UW-E30-020004		REV B

LOOP WIRING DIAGRAM / POLISHING LOOP






FIELD INSTRUMENT JUNCTION BOX PANEL TERMINAL BLOCK I/O MODULE

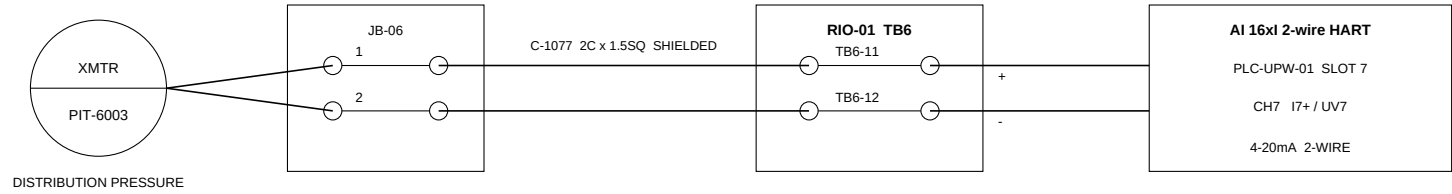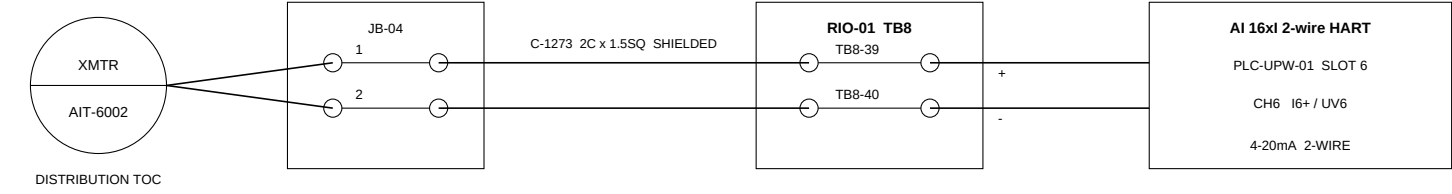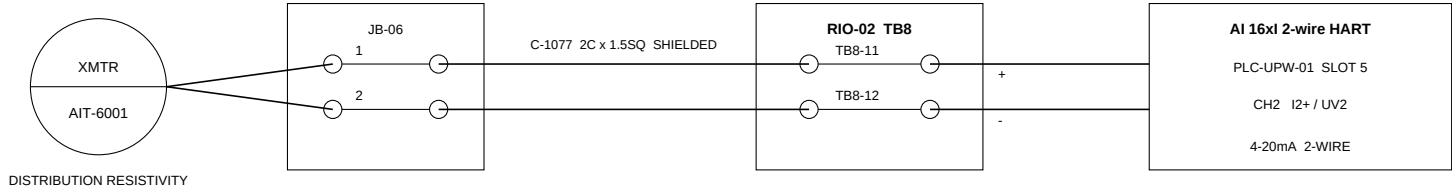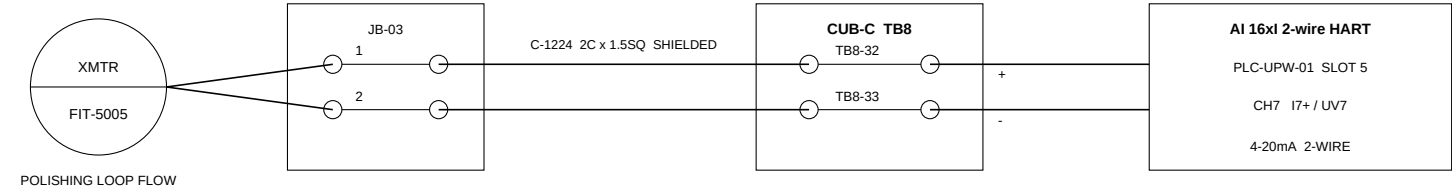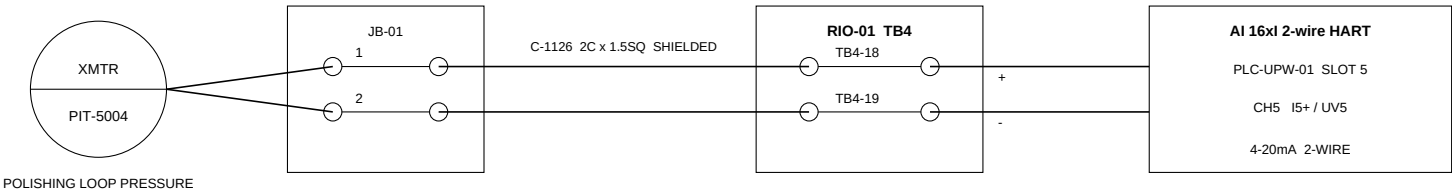

REV B ISSUED FOR APPROVAL 26-05-20 DEM	
DWG. TITLE	DEMO UPW SYSTEM LOOP WIRING DIAGRAM FOR POLISHING LOOP
PROJECT TITLE	DEMO WATER PLANT Ph1
PROJECT NO.	99001D
MAKER	DEMO ENGINEERING CO., LTD.
SHEET NO.	DM-PNT1C01-UW-E30-020005
REV B	

LOOP WIRING DIAGRAM / DISTRIBUTION


FIELD INSTRUMENT JUNCTION BOX PANEL TERMINAL BLOCK I/O MODULE

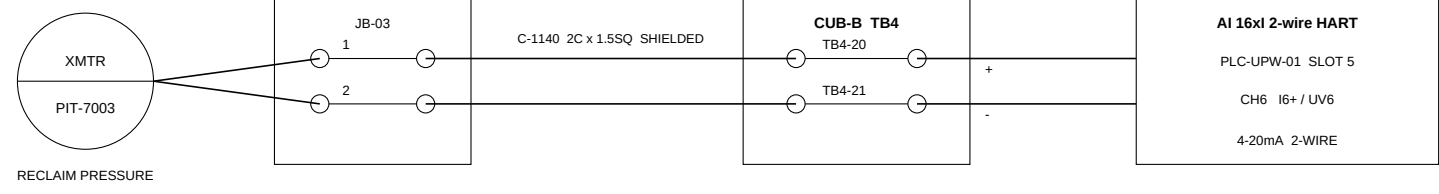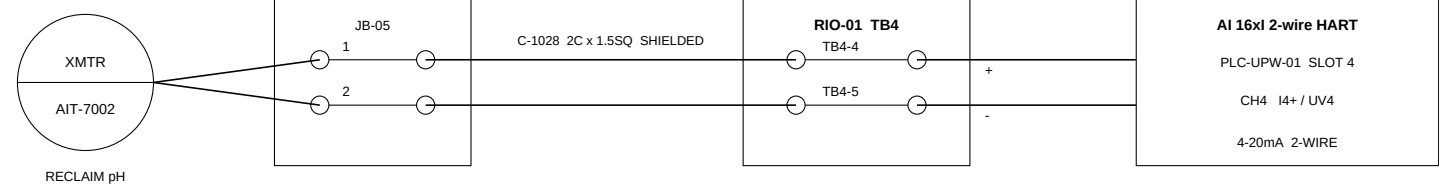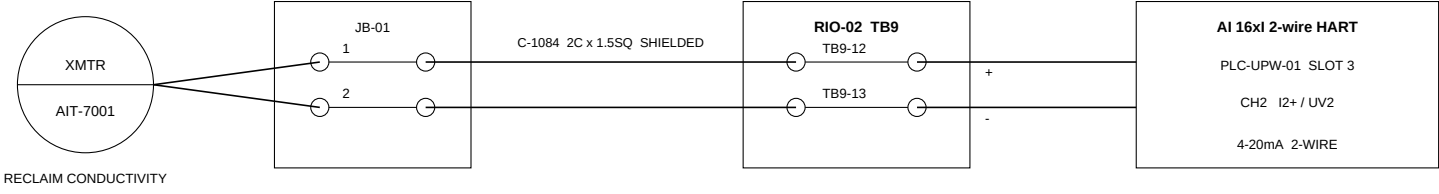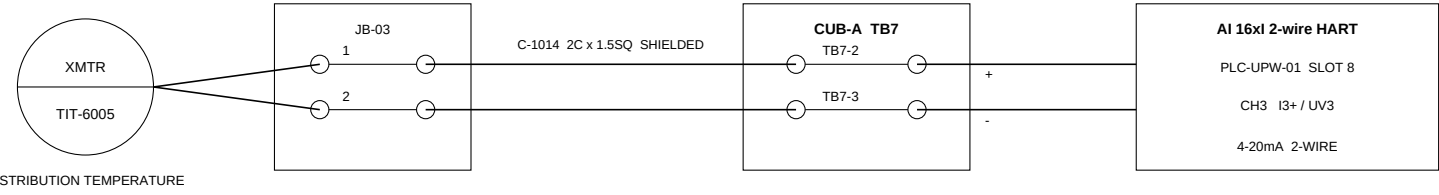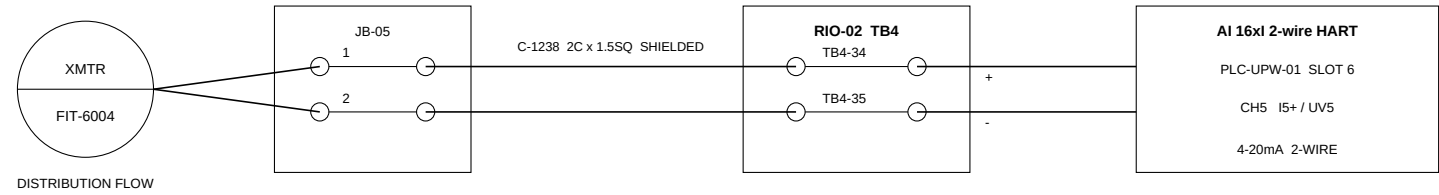

REV B ISSUED FOR APPROVAL 26-05-20 DEM	
DWG. TITLE	DEMO UPW SYSTEM LOOP WIRING DIAGRAM FOR DISTRIBUTION
PROJECT TITLE	DEMO WATER PLANT Ph1
PROJECT NO.	99001D
MAKER	DEMO ENGINEERING CO., LTD.
SHEET NO.	DM-PNT1C01-UW-E30-020006
REV B	

LOOP WIRING DIAGRAM / RECLAIM






FIELD INSTRUMENT JUNCTION BOX PANEL TERMINAL BLOCK I/O MODULE

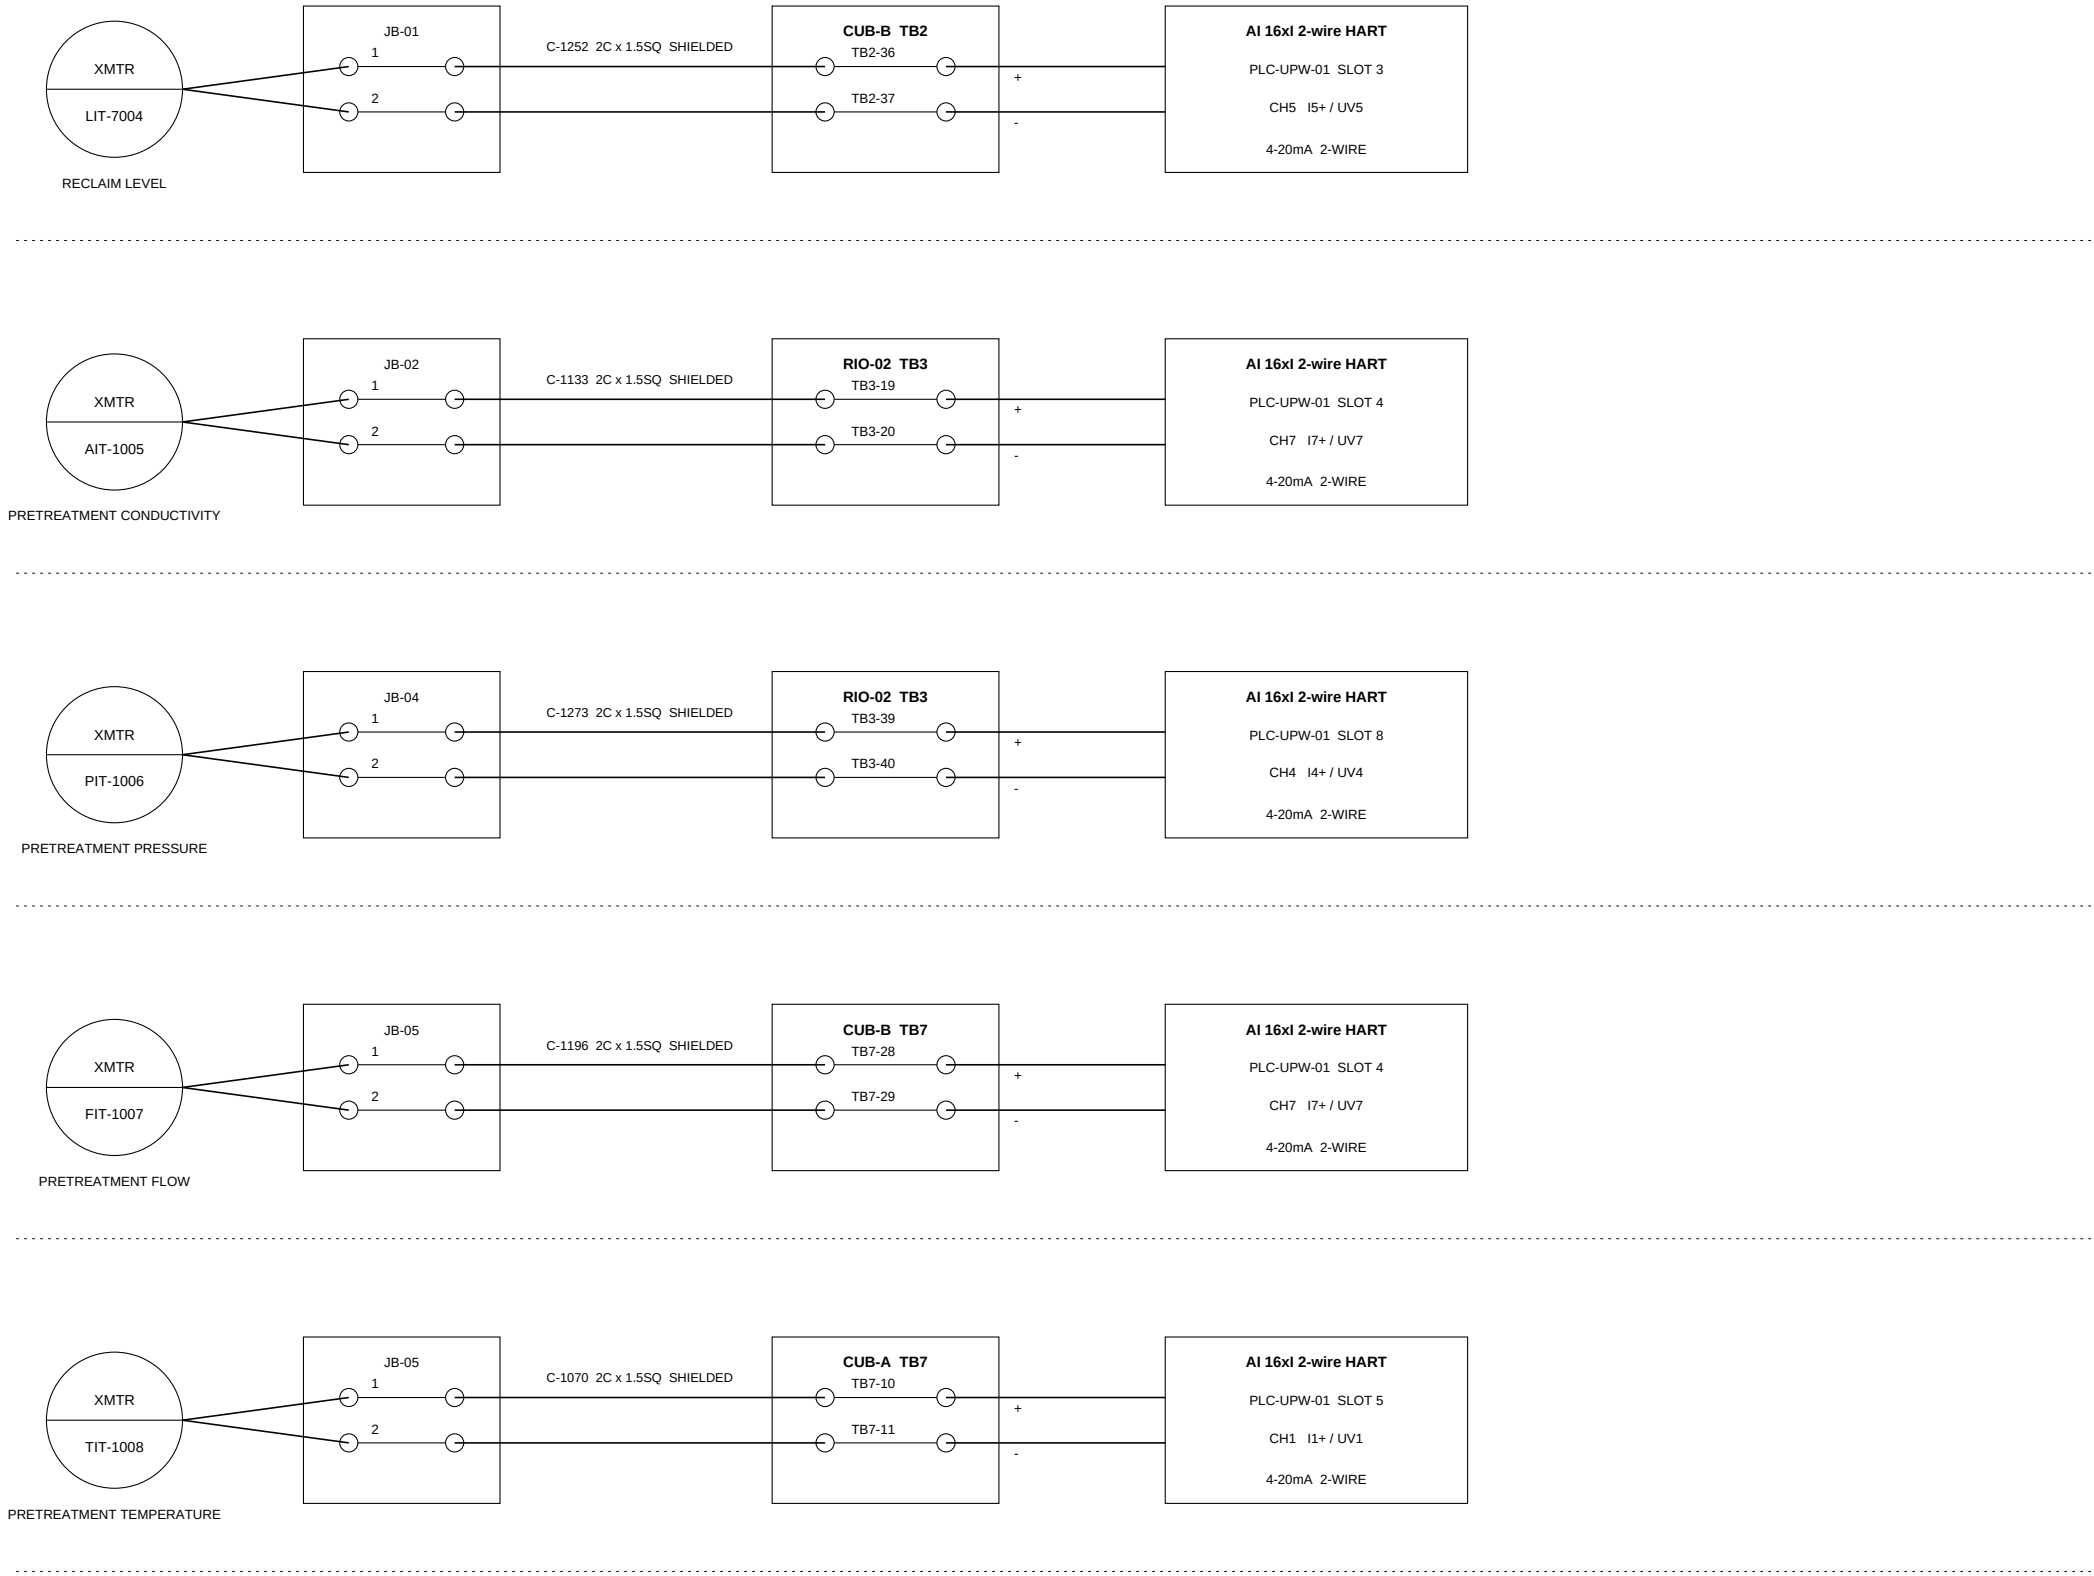

REV B	ISSUED FOR APPROVAL	26-05-20	DEM
DWG. TITLE	DEMO UPW SYSTEM LOOP WIRING DIAGRAM FOR RECLAIM		
PROJECT TITLE	DEMO WATER PLANT Ph1		
PROJECT NO.	99001D		
MAKER	DEMO ENGINEERING CO., LTD.		
SHEET NO.	DM-PNT1C01-UW-E30-020007		REV B

LOOP WIRING DIAGRAM / RO SYSTEM






FIELD INSTRUMENT JUNCTION BOX PANEL TERMINAL BLOCK I/O MODULE

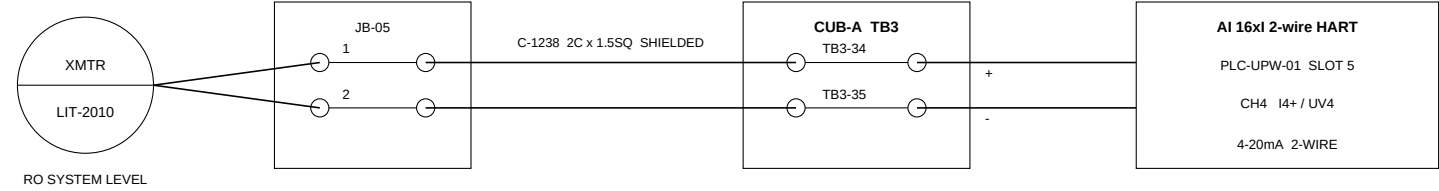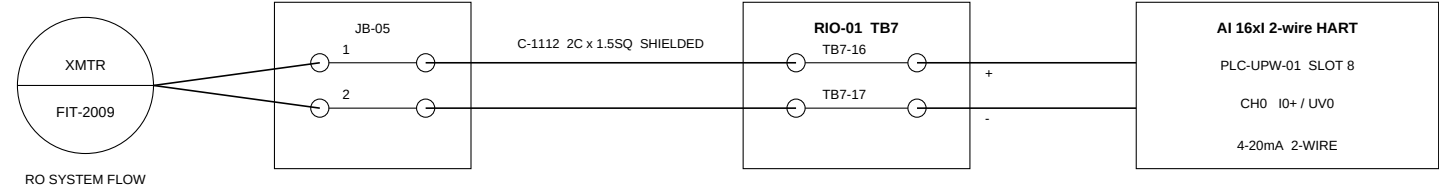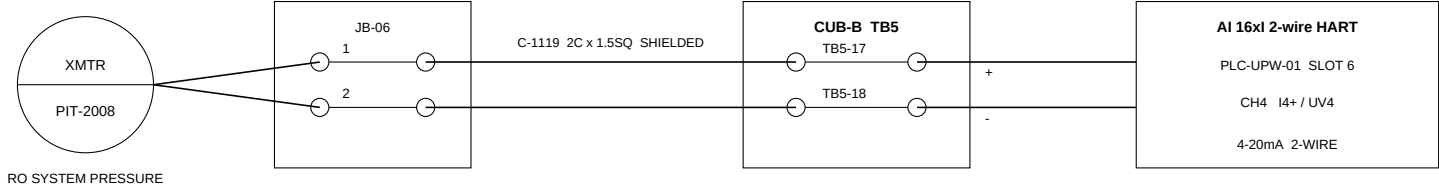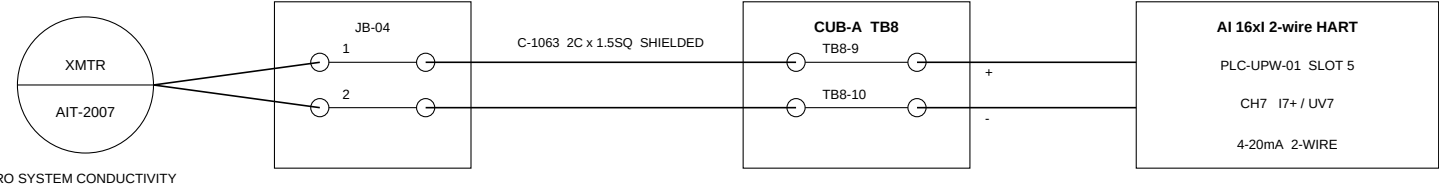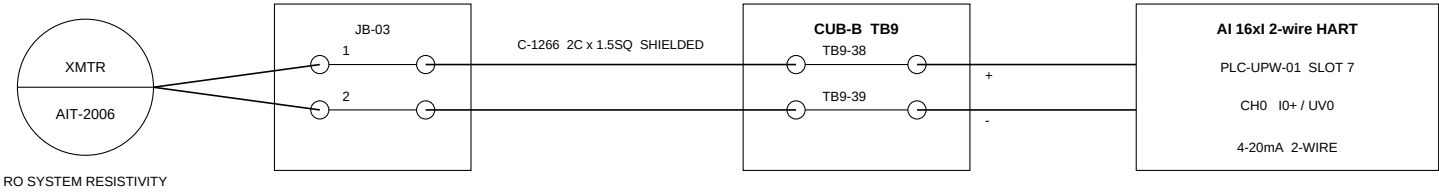

REV B ISSUED FOR APPROVAL 26-05-20 DEM			
DWG. TITLE	DEMO UPW SYSTEM LOOP WIRING DIAGRAM FOR RO SYSTEM		
PROJECT TITLE	DEMO WATER PLANT Ph1		
PROJECT NO.	99001D		
MAKER	DEMO ENGINEERING CO., LTD.		
SHEET NO.	DM-PNT1C01-UW-E30-020008		REV B

LOOP WIRING DIAGRAM / CEDI SYSTEM

FIELD INSTRUMENT JUNCTION BOX PANEL TERMINAL BLOCK I/O MODULE

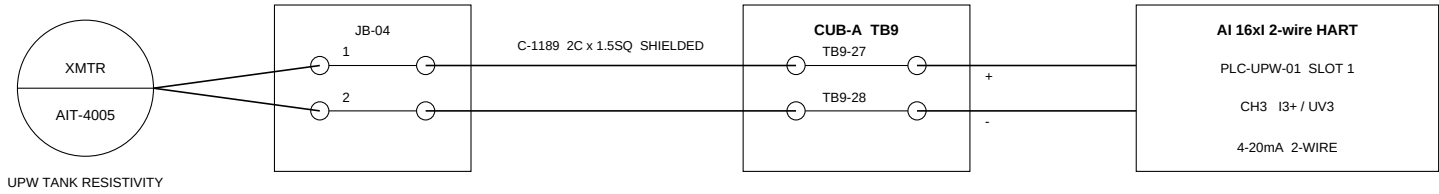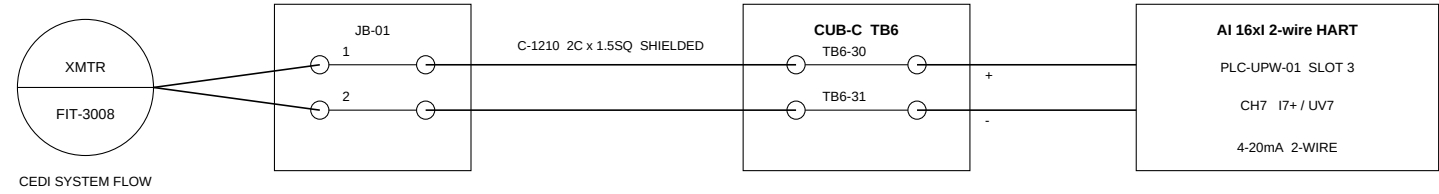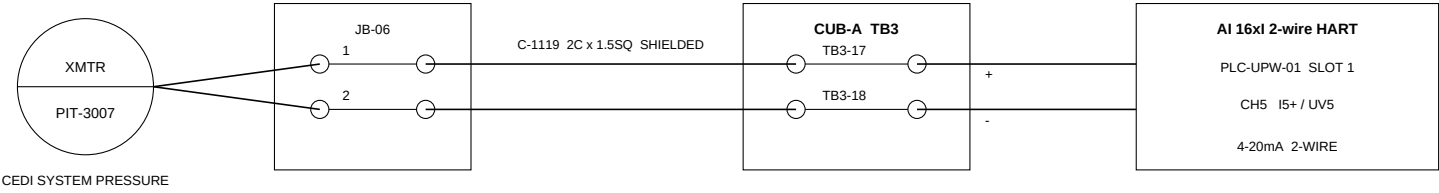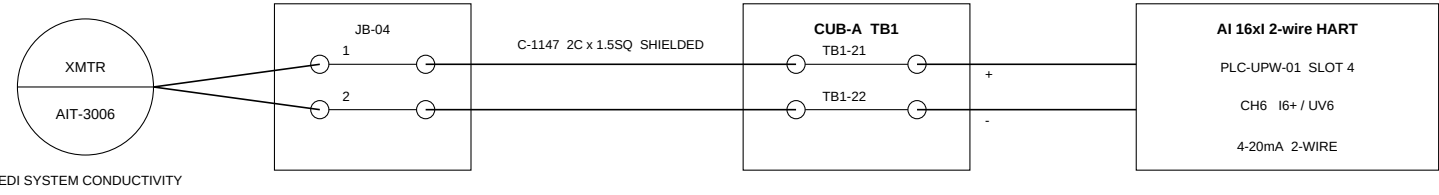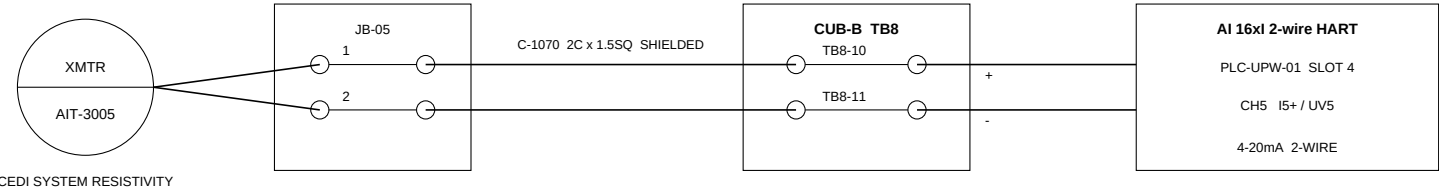

REV B ISSUED FOR APPROVAL 26-05-20 DEM

DWG. TITLE DEMO UPW SYSTEM
LOOP WIRING DIAGRAM FOR
CEDI SYSTEM

PROJECT TITLE DEMO WATER PLANT Ph1

PROJECT NO. 99001D






MAKER DEMO ENGINEERING CO., LTD.

SHEET NO. DM-PNT1C01-UW-E30-020009

REV B

LOOP WIRING DIAGRAM / UPW TANK






FIELD INSTRUMENT JUNCTION BOX PANEL TERMINAL BLOCK I/O MODULE

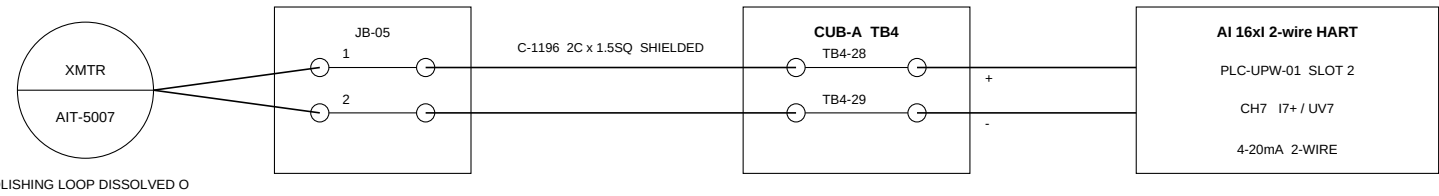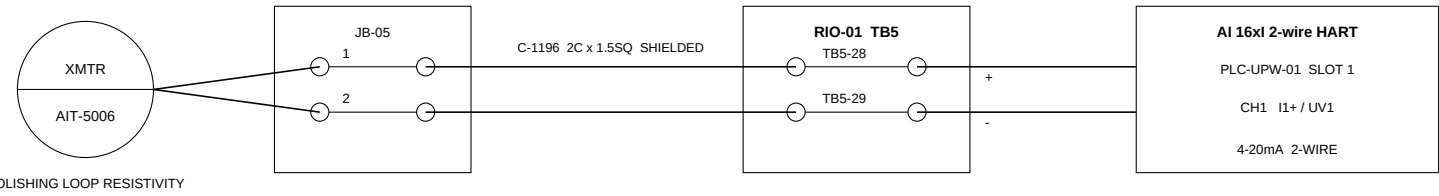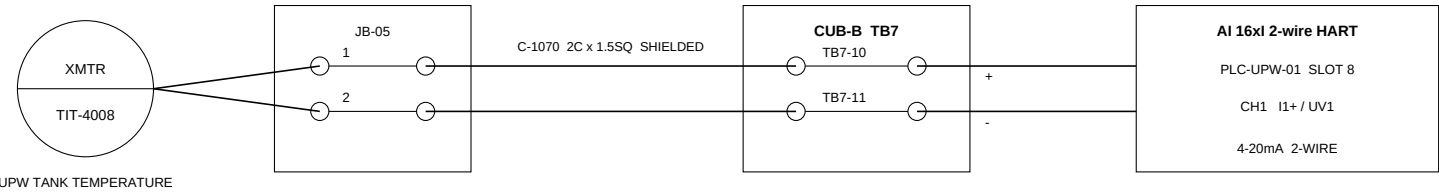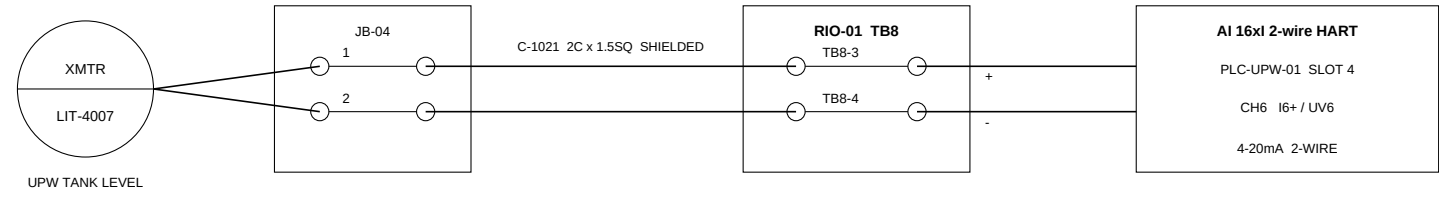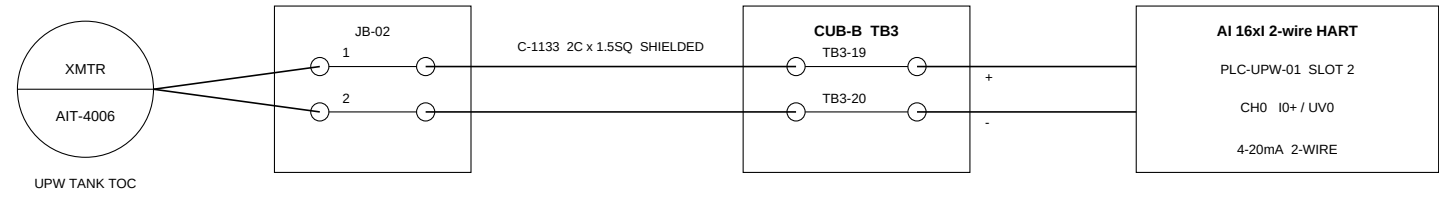

REV B ISSUED FOR APPROVAL 26-05-20 DEM	
DWG. TITLE	DEMO UPW SYSTEM LOOP WIRING DIAGRAM FOR UPW TANK
PROJECT TITLE	DEMO WATER PLANT Ph1
PROJECT NO.	99001D
MAKER	DEMO ENGINEERING CO., LTD.
SHEET NO.	DM-PNT1C01-UW-E30-020010
REV B	

LOOP WIRING DIAGRAM / POLISHING LOOP






FIELD INSTRUMENT JUNCTION BOX PANEL TERMINAL BLOCK I/O MODULE

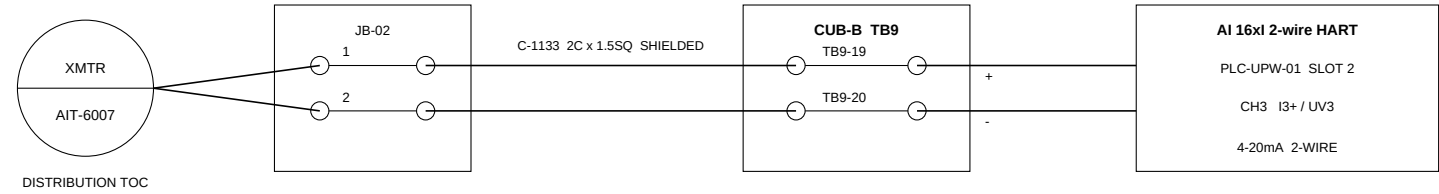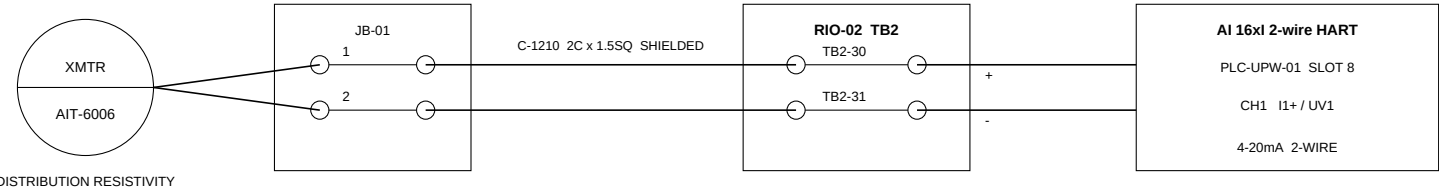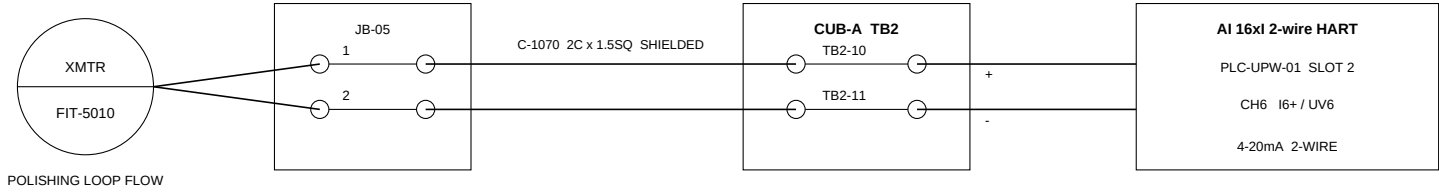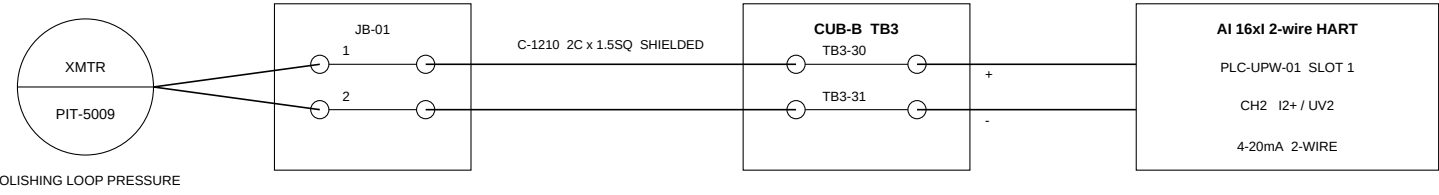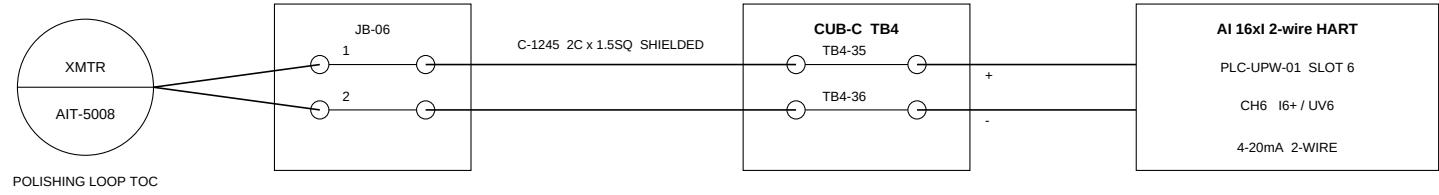

REV B	ISSUED FOR APPROVAL	26-05-20	DEM
DWG. TITLE	DEMO UPW SYSTEM LOOP WIRING DIAGRAM FOR POLISHING LOOP		
PROJECT TITLE	DEMO WATER PLANT Ph1		
PROJECT NO.	99001D		
MAKER	DEMO ENGINEERING CO., LTD.		
SHEET NO.	DM-PNT1C01-UW-E30-020011		REV B

LOOP WIRING DIAGRAM / DISTRIBUTION


FIELD INSTRUMENT JUNCTION BOX PANEL TERMINAL BLOCK I/O MODULE

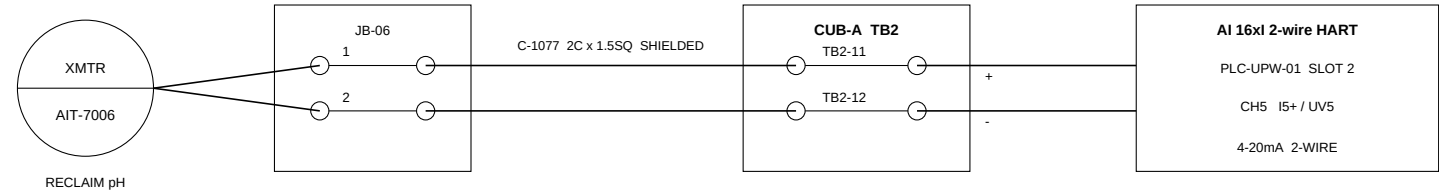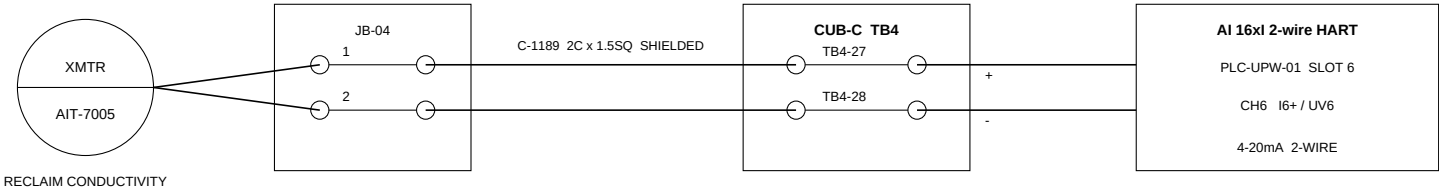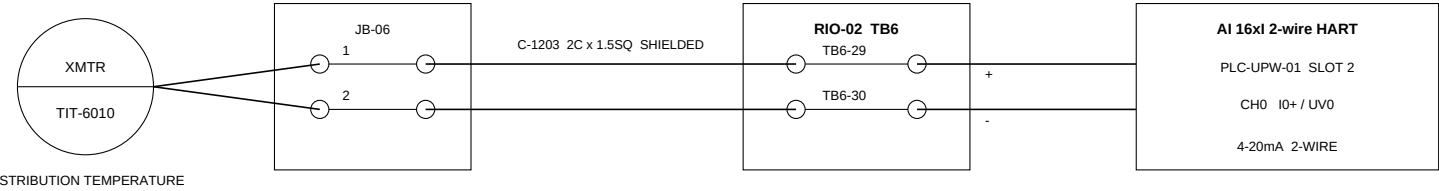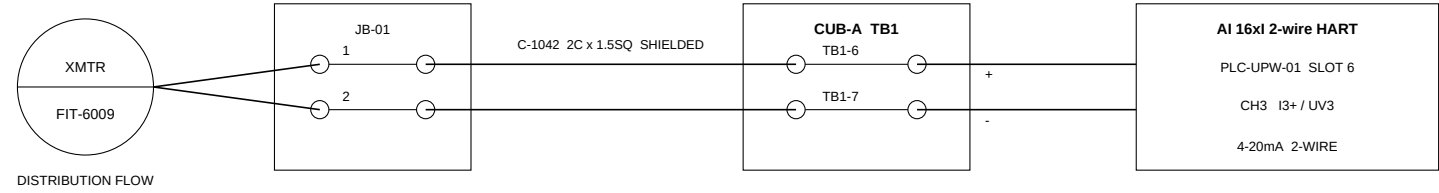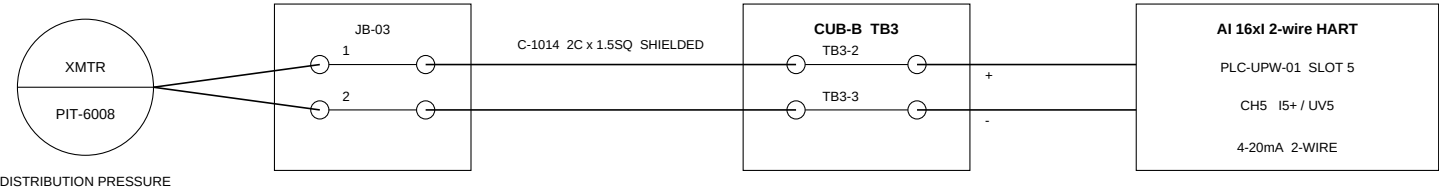

REV B ISSUED FOR APPROVAL 26-05-20 DEM	
DWG. TITLE	DEMO UPW SYSTEM LOOP WIRING DIAGRAM FOR DISTRIBUTION
PROJECT TITLE	DEMO WATER PLANT Ph1
PROJECT NO.	99001D
MAKER	DEMO ENGINEERING CO., LTD.
SHEET NO.	DM-PNT1C01-UW-E30-020012
REV B	

LOOP WIRING DIAGRAM / RECLAIM


FIELD INSTRUMENT JUNCTION BOX PANEL TERMINAL BLOCK I/O MODULE

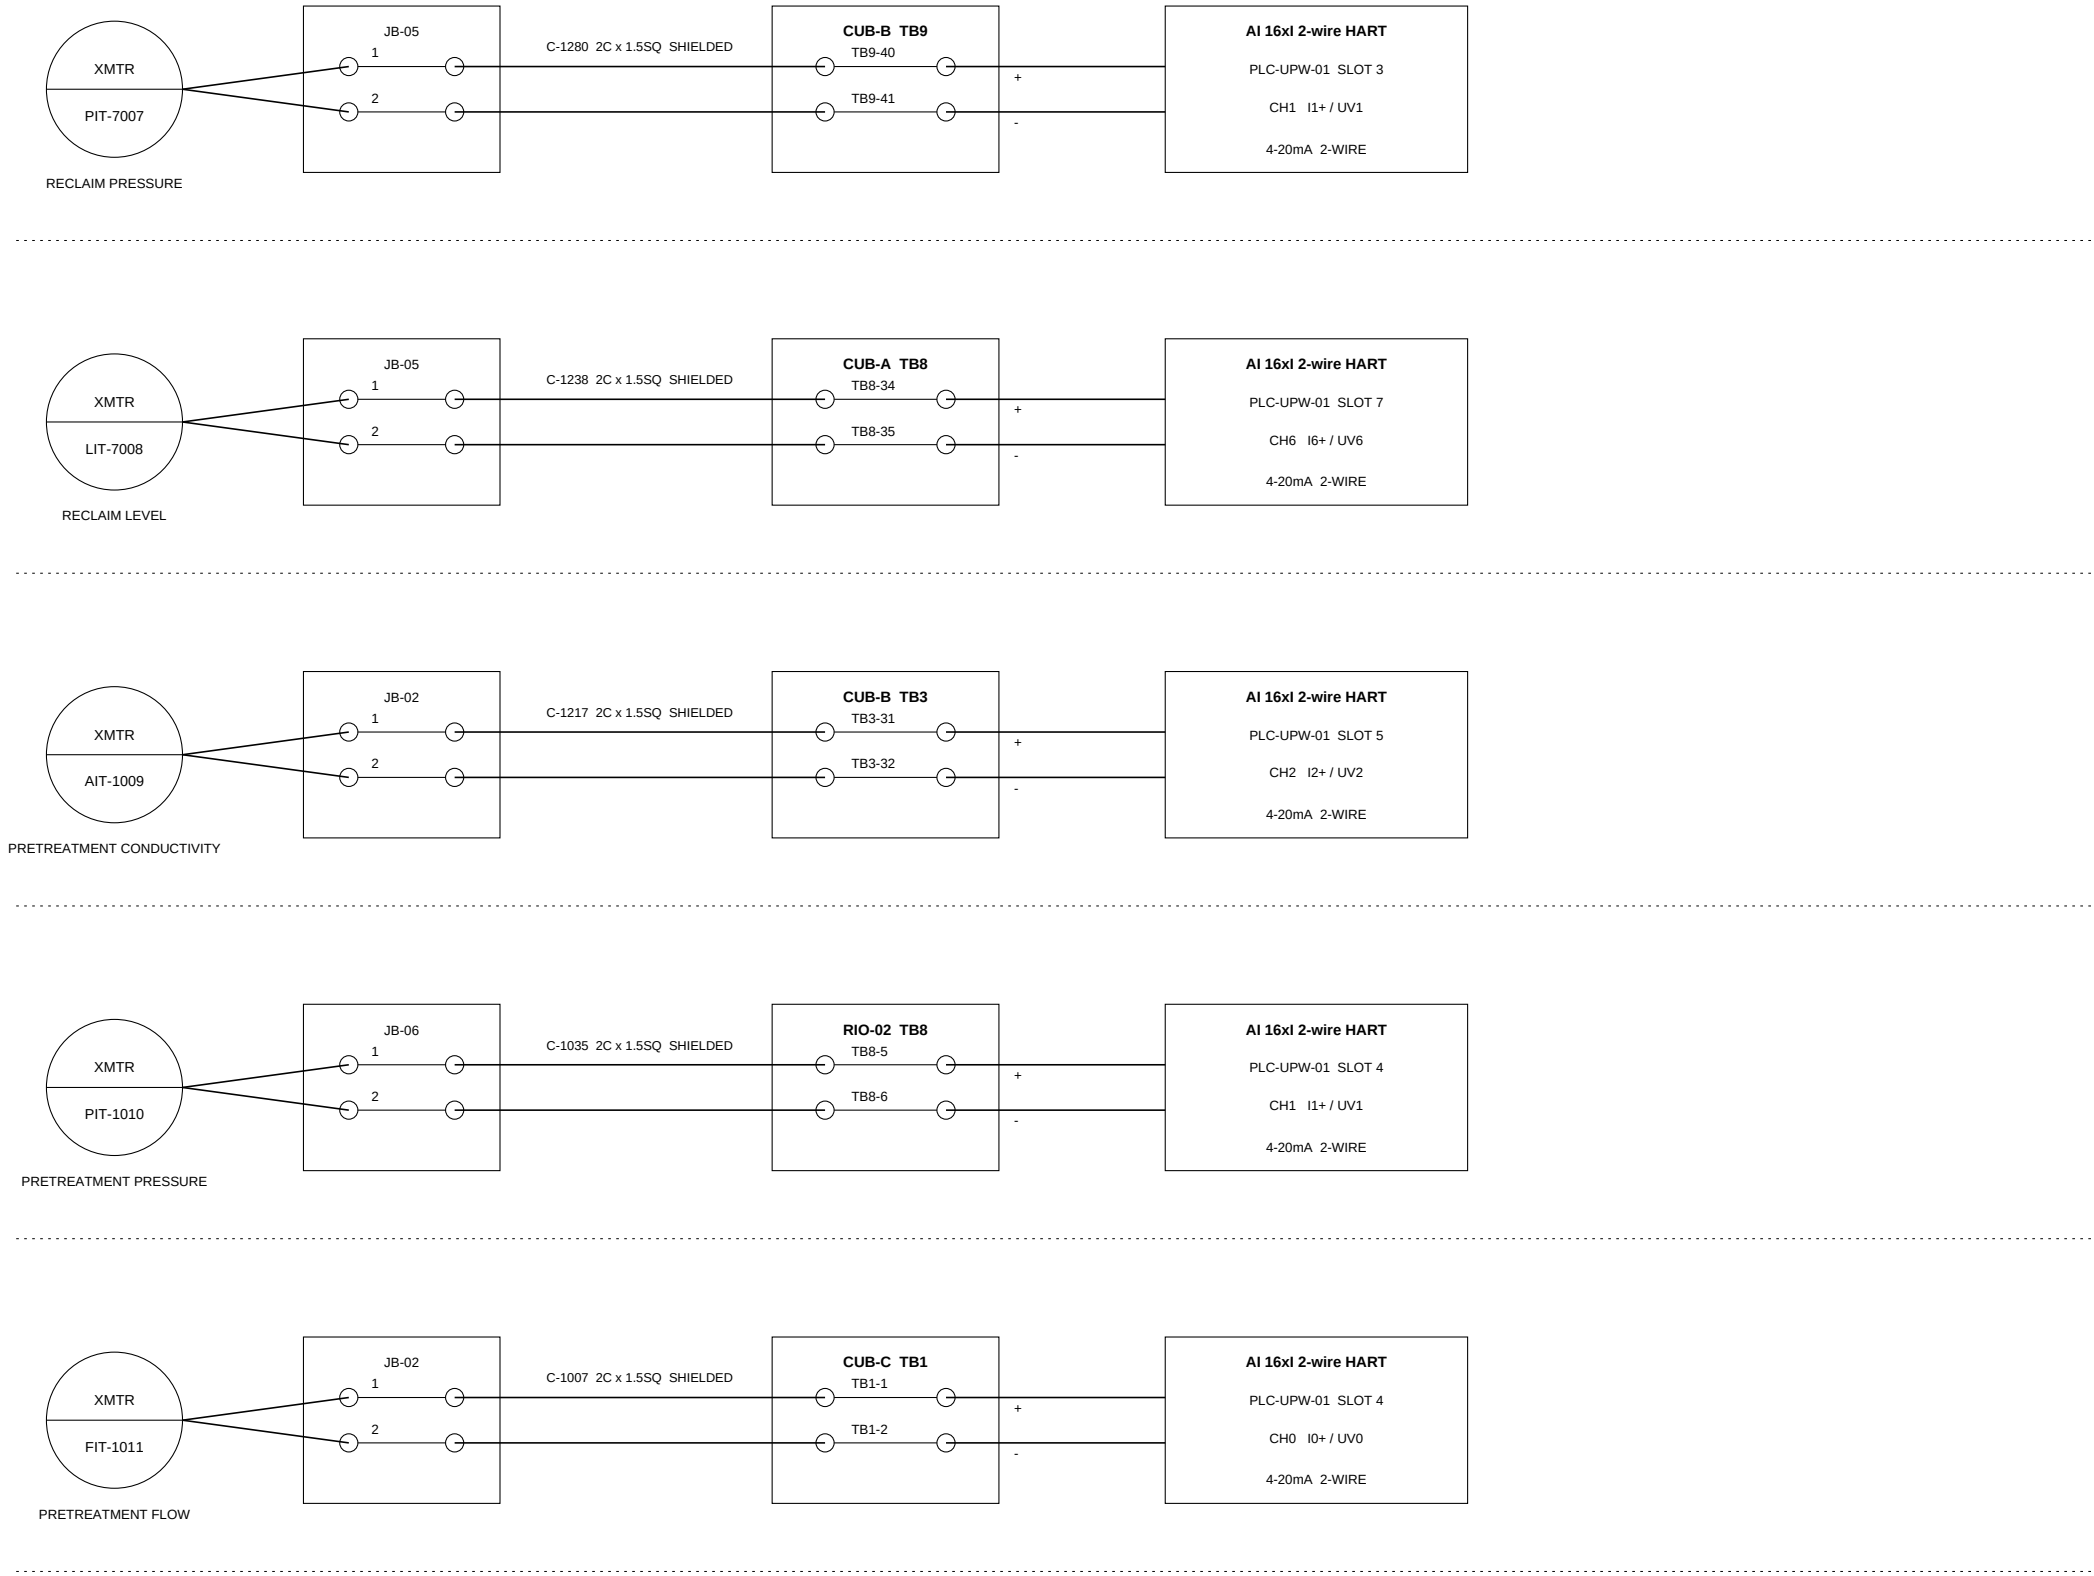


REV B ISSUED FOR APPROVAL 26-05-20 DEM			
DWG. TITLE	DEMO UPW SYSTEM LOOP WIRING DIAGRAM FOR RECLAIM		
PROJECT TITLE	DEMO WATER PLANT Ph1		
PROJECT NO.	99001D		
MAKER	DEMO ENGINEERING CO., LTD.		
SHEET NO.	DM-PNT1C01-UW-E30-020013		REV B

LOOP WIRING DIAGRAM / PRETREATMENT


FIELD INSTRUMENT JUNCTION BOX PANEL TERMINAL BLOCK I/O MODULE

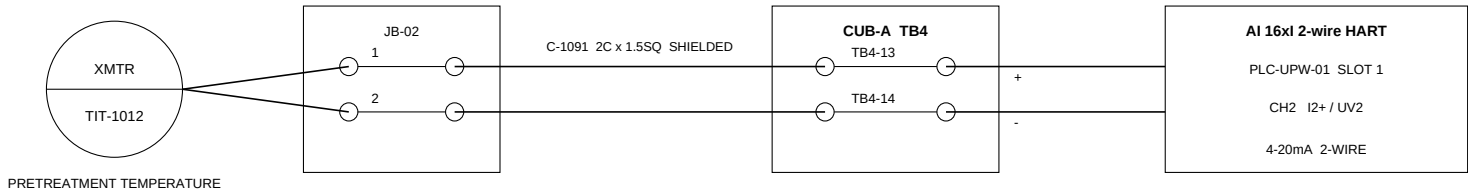


PRETREATMENT TEMPERATURE

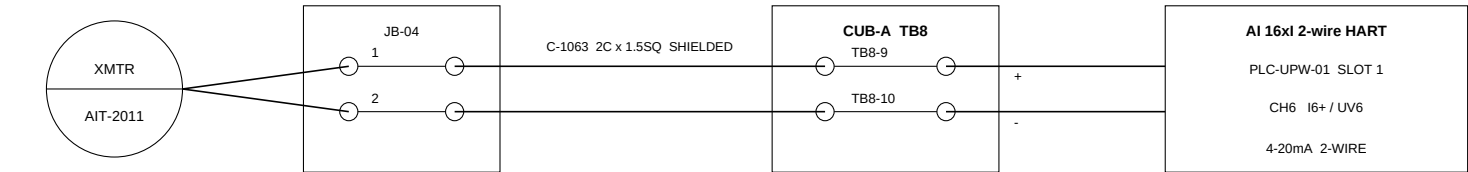


RO SYSTEM RESISTIVITY

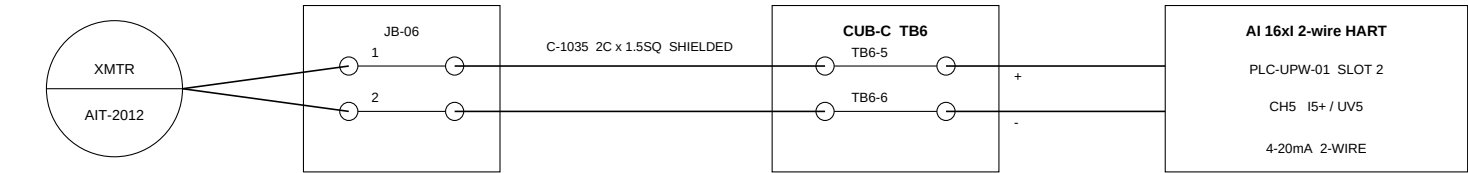

RO SYSTEM CONDUCTIVITY

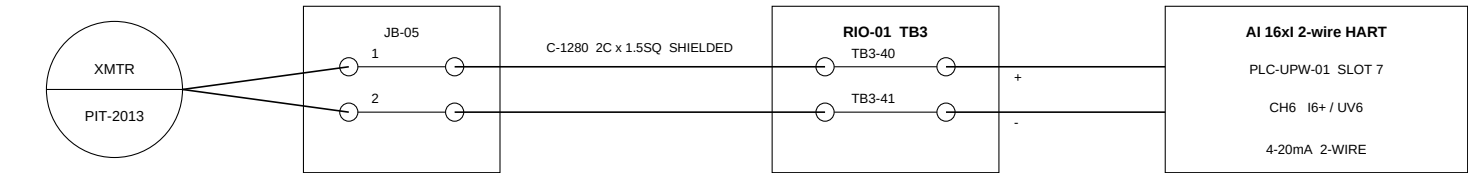

RO SYSTEM PRESSURE

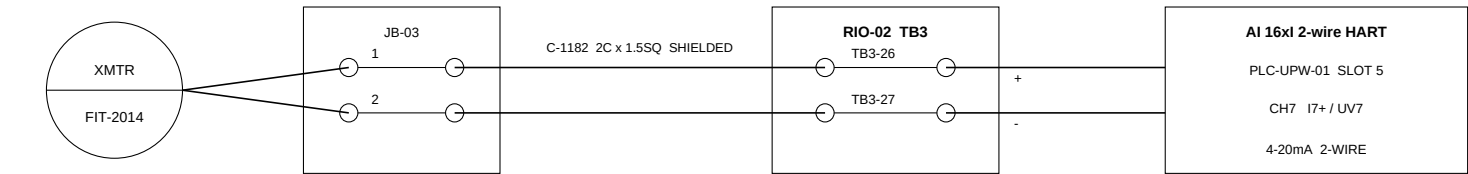

RO SYSTEM FLOW

REV B ISSUED FOR APPROVAL 26-05-20 DEM

DWG. TITLE DEMO UPW SYSTEM
LOOP WIRING DIAGRAM FOR
PRETREATMENT

PROJECT TITLE DEMO WATER PLANT Ph1

PROJECT NO. 99001D



MAKER DEMO ENGINEERING CO., LTD.

SHEET NO. DM-PNT1C01-UW-E30-020014

REV B

LOOP WIRING DIAGRAM / RO SYSTEM

FIELD INSTRUMENT JUNCTION BOX PANEL TERMINAL BLOCK I/O MODULE

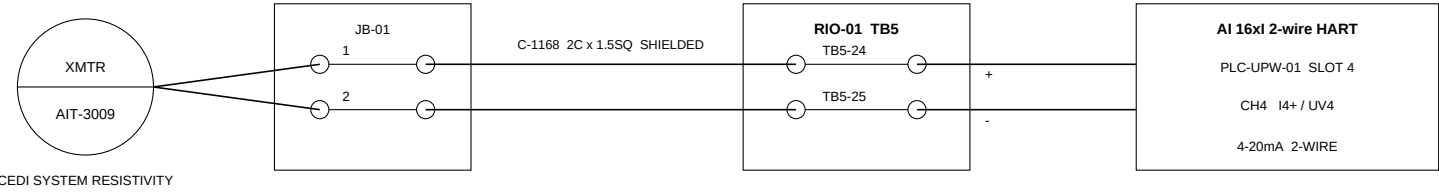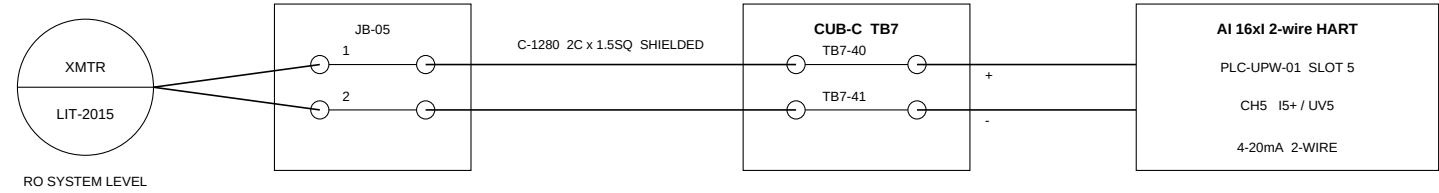

REV B ISSUED FOR APPROVAL 26-05-20 DEM			
DWG. TITLE	DEMO UPW SYSTEM LOOP WIRING DIAGRAM FOR RO SYSTEM		
PROJECT TITLE	DEMO WATER PLANT Ph1		
PROJECT NO.	99001D		
MAKER	DEMO ENGINEERING CO., LTD.		
SHEET NO.	DM-PNT1C01-UW-E30-020015		REV B